



بسمه تعالی

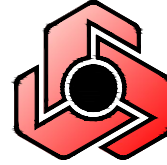

بانک ملت - اداره کل مهندسی ساختمان (واحد طراحی و نظارت)


عنوان پروژه : لابی منفی فرصت

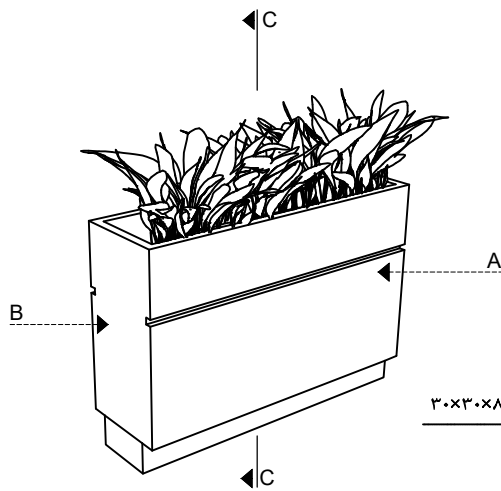

نمای سه بعدی


صرفاً به جهت درک بهتر طرح ارائه شده است
ملاک ابعاد و نقشه های دو بعدی خواهد بود.

گلدان پلاستیکی به ابعاد ۳۰×۳۰×۸۰

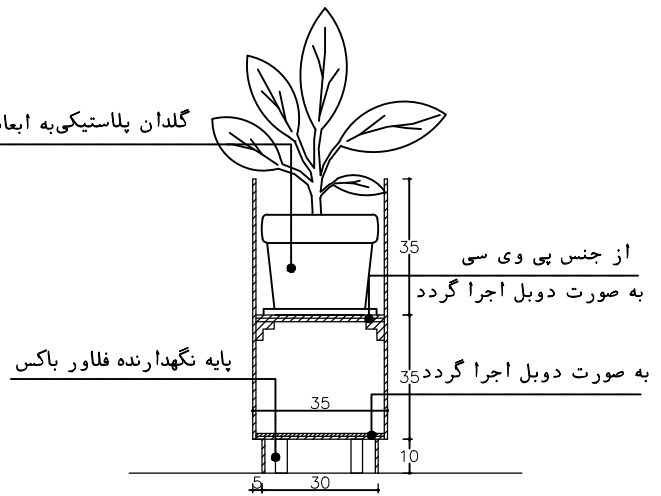

مقطع فلاور باکس C-C


SC 1:5

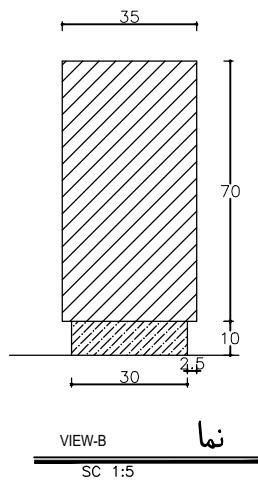

VIEW-B

نما

SC 1:5

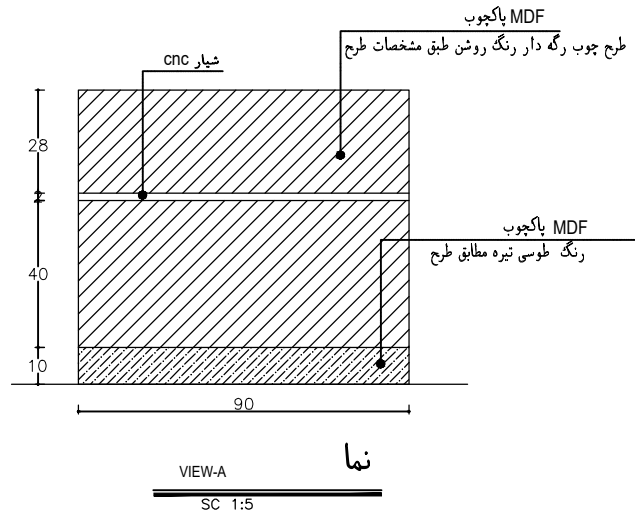

VIEW-A


نما

SC 1:5


توجه:

پیمانکار موظف است قبل از اجرا اندازه های وضع موجود را
برداشت کرده و با طرح تطبیق دهد.


تغییرات		شماره کلامبرتری:	
تاریخ	امضاء	تاریخ	امضاء
پانک ملت - اداره کل مهندسی ساختمان (واحد طراحی و نظارت)		عنوان پروژه: طبقه منفی یک ساختمان مرکزی فرصت	
رشته: معماری		عنوان نقشه: طراحی لابی طبقه منفی یک فرصت	
تاریخ	امضاء	تاریخ	امضاء
۱۳۹۴/۴/۹	امیری زاده	طراح	امیری زاده
۱۳۹۴/۴/۹	امیری زاده	ترسیم	امیری زاده
		کنترل	
		تصویب	
مهندس: طبین نقشه		شماره نقشه: A-04	

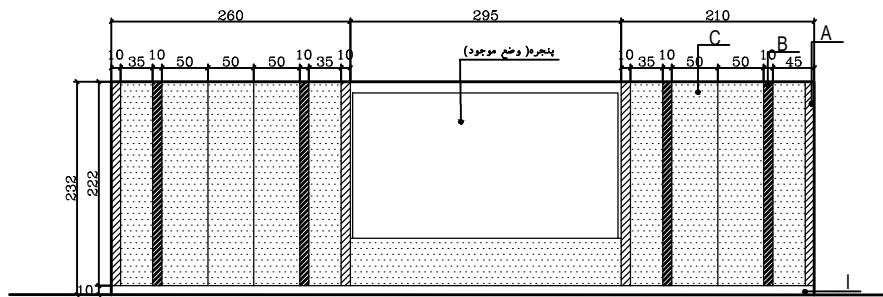


VIEW-A
SCALE 1:20

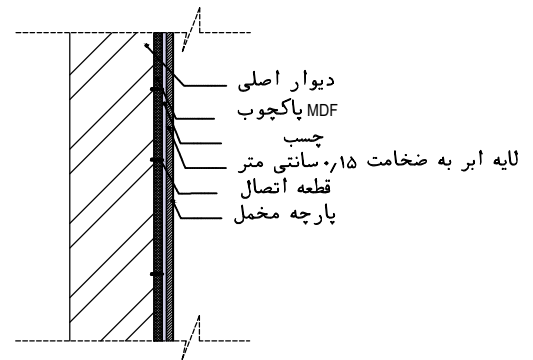

مقطع دیوار لمسه کوبی
SC 1:5

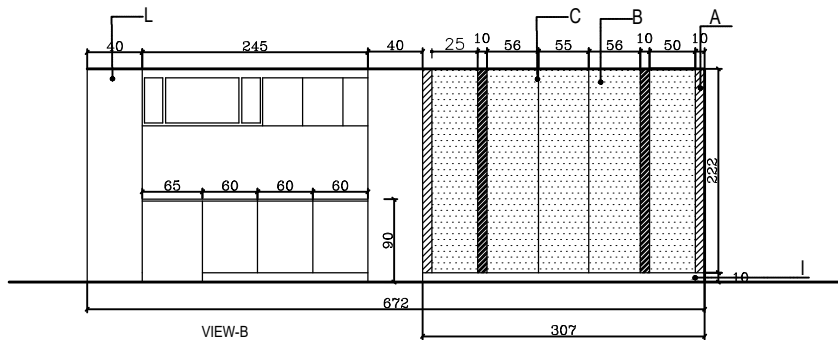


VIEW-B
SCALE 1:20

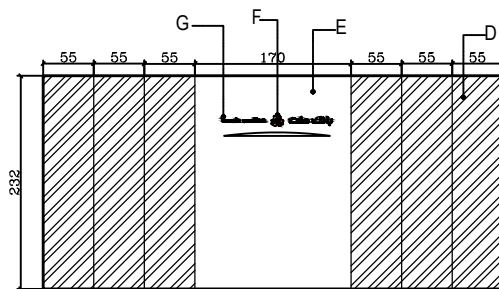

VIEW-C
SC 1:20


کد	م مصالح	رنگ	کد رنگ
A	نوار استیل	طلایی	
B	نوار استیل	دودی براق	
C	پارچه لمسه کوبی	طوسی کرم روشن	
D	MDF پاکچوب	رنگ دار روشن	
E	سرامیک برند pma یوک میچ	مطابق طرح	به ابعاد ۲۸×۱۲۰
F	لوگوی بانک از پلکسی گلاس ضخامت ۶ میلیمتر (لوگو فریز مطابق طرح و رنگ سازمانی)	نارنجی	RAL Code: 1028
G	لوگو نوشته بانک از پلکسی گلاس ضخامت ۶ میلیمتر	قرمز	RAL Code: 3020
		سفید	RAL Code: 9016
I	فرنیز پی وی سی	خاکستری تیره	
L	کابینت بلایرایی مطابق جزئیات		
M	لاکوبل مشکی وضع موجود		

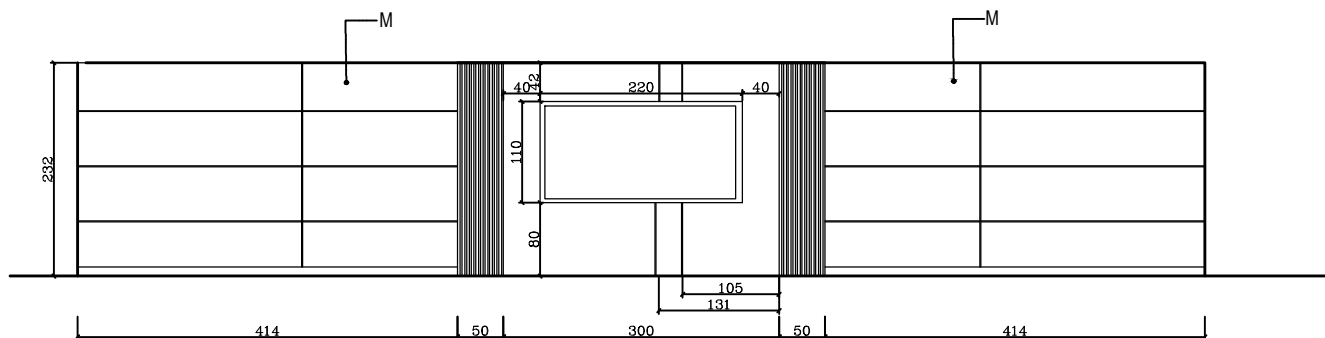

VIEW-D
SC 1:20


توجه:

پیمانکار موظف است قبل از اجرا نمونه تمامی متریال های مصرفی را به تایید طراح و ناظر پروژه برساند.
پیمانکار موظف است قبل از اجرا اندازه های وضع موجود را برداشت کرده و با طرح تطبیق دهد.

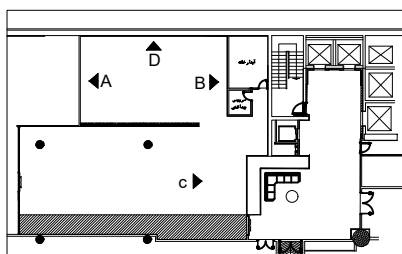


پلان راهنما

تغییرات	تاریخ	امضاء	تاریخ	امضاء
شماره کادربندی:				
بانک ملت - اداره کل مهندسی ساختمان (واحد طراحی و نظارت)				
عنوان پروژه: طبقه منفی یک ساختمان مرکزی فرصت				
عنوان نقشه: طراحی لابی طبقه منفی یک فرصت				
شماره نقشه: A-05				
طراحی: طراح				
تصویر: تصویر				
تاریخ: ۱۳۹۴/۰۹/۰۹				
امضاء: امیری زاده				
تاریخ: ۱۳۹۴/۰۹/۰۹				
امضاء: امیری زاده				

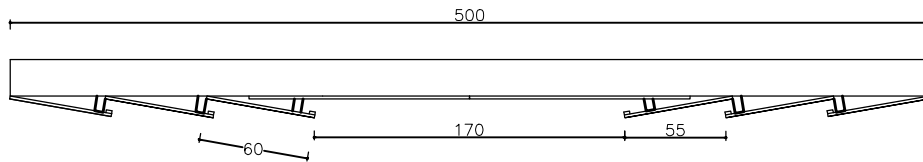


پلان دیوار پشت پذیرش

SC 1:10

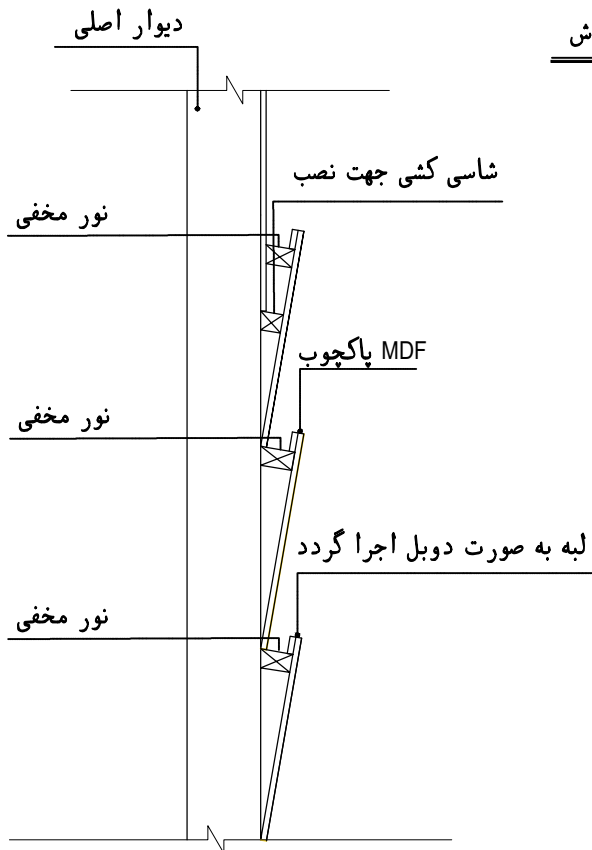


پلان

SC 1:5

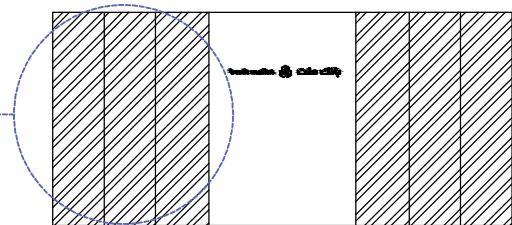

VIEW-C

SC 1:20

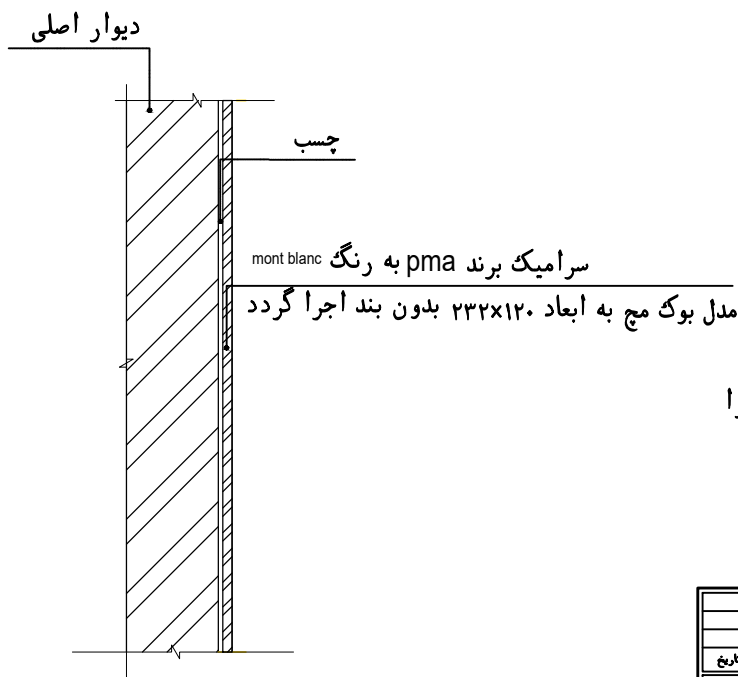

نحوه اتصال سرامیک به دیوار


SC 1:5

توجه:

پیمانکار موظف است قبل از اجرا اندازه های وضع موجود را برداشت کرده و با طرح تطبیق دهد.




قبل از اجرا سطح دیوار ترمیم و صاف باشد.

تاریخ		مختصات		شماره کادربرداری:	
تاریخ	امضاء	تاریخ	امضاء	بانک ملت - اداره کل مهندسی ساختمان (واحد طراحی و نظارت)	
معماری		رشته:		عنوان پروژه: طبقه منفی یک ساختمان مرکزی فرصت	
تاریخ	امضاء	طراح	امضاء	عنوان نقشه: طراحی لابی طبقه منفی یک فرصت	
۱۴۰۴/۰۹	امیری زاده	تصویر	امیری زاده	طراح: لابی طبقه منفی یک فرصت	
۱۴۰۴/۰۹	امیری زاده	کنترل	امیری زاده	تصویر	
مختصات		شماره نقشه: A-06		شماره نقشه: A-06	

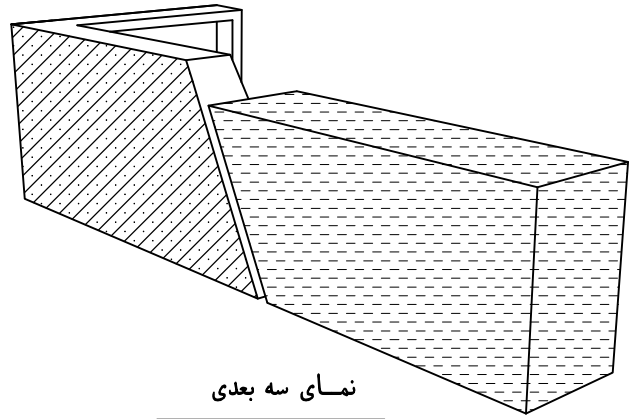


نمای سه بعدی


مرا به جهت درگ بهتر طرح ارائه شده است
ملاک ایجاد و نقشه های دو بدی خواهد بود.

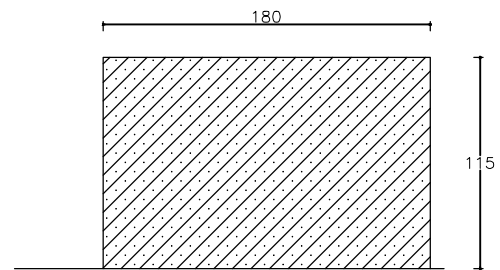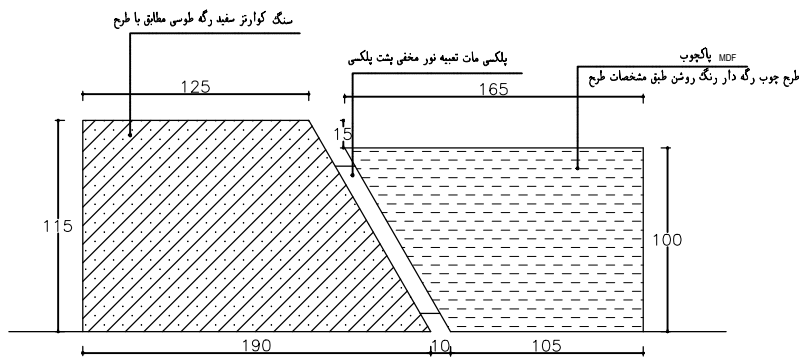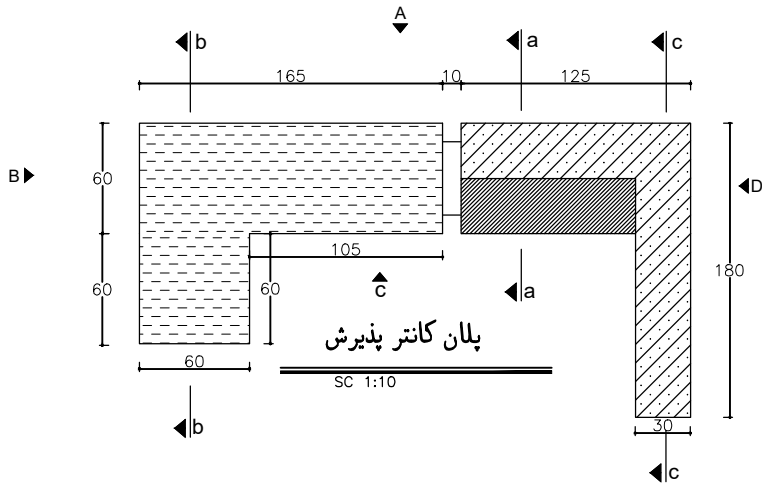

لبه ها به صورت دابل اجرا گردد (۱۰ سانتی متر برگشت)

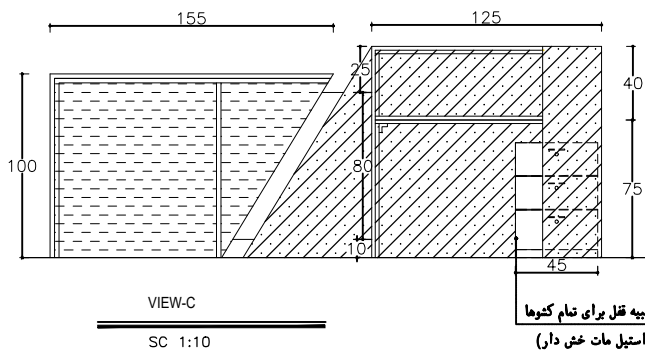

پوینت متحرک از نوع متریال کانتر و تمیبه قل برای تمام کتوها
(دستگیره به طول ۱۰ سانتیمتر از استیل مات غش دار)





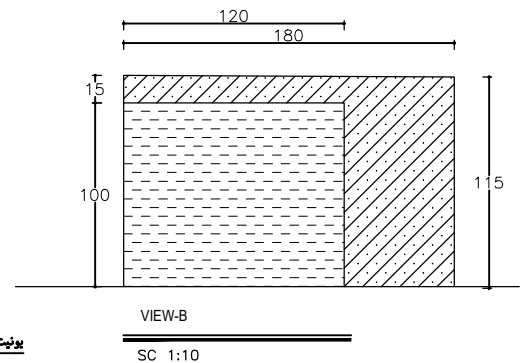


توجه:

پیمانکار موظف است قبل از اجرا اندازه های وضع موجود را
برداشت کرده و با طرح تطبیق دهد.




پیمانکار موظف است قبل از اجرا نمونه تمامی متریال های مصرفی را به تایید طراح و ناظر برساند.

تاییدات		شماره کلامبرتری:	
امضاء	تاریخ	امضاء	تاریخ
پانک ملت - اداره کل مهندسی ساختمان (واحد طراحی و نظارت)		عنوان پروژه: طبقه منفی یک ساختمان مرکزی فرصت	
عنوان نقشه:		طراحی ایلی طبقه منفی یک فرصت	
شماره نقشه: A-07		عنوان نقشه: طراحی ایلی طبقه منفی یک فرصت	
مهندس: طبق نقشه		عنوان نقشه: طراحی ایلی طبقه منفی یک فرصت	
تاریخ		امضاء	تاریخ
۱۳۹۴/۴/۹	۱۳۹۴/۴/۹	امیر زاده	طراح
۱۳۹۴/۴/۹	۱۳۹۴/۴/۹	امیر زاده	ترسیم
		کنترل	تصویب

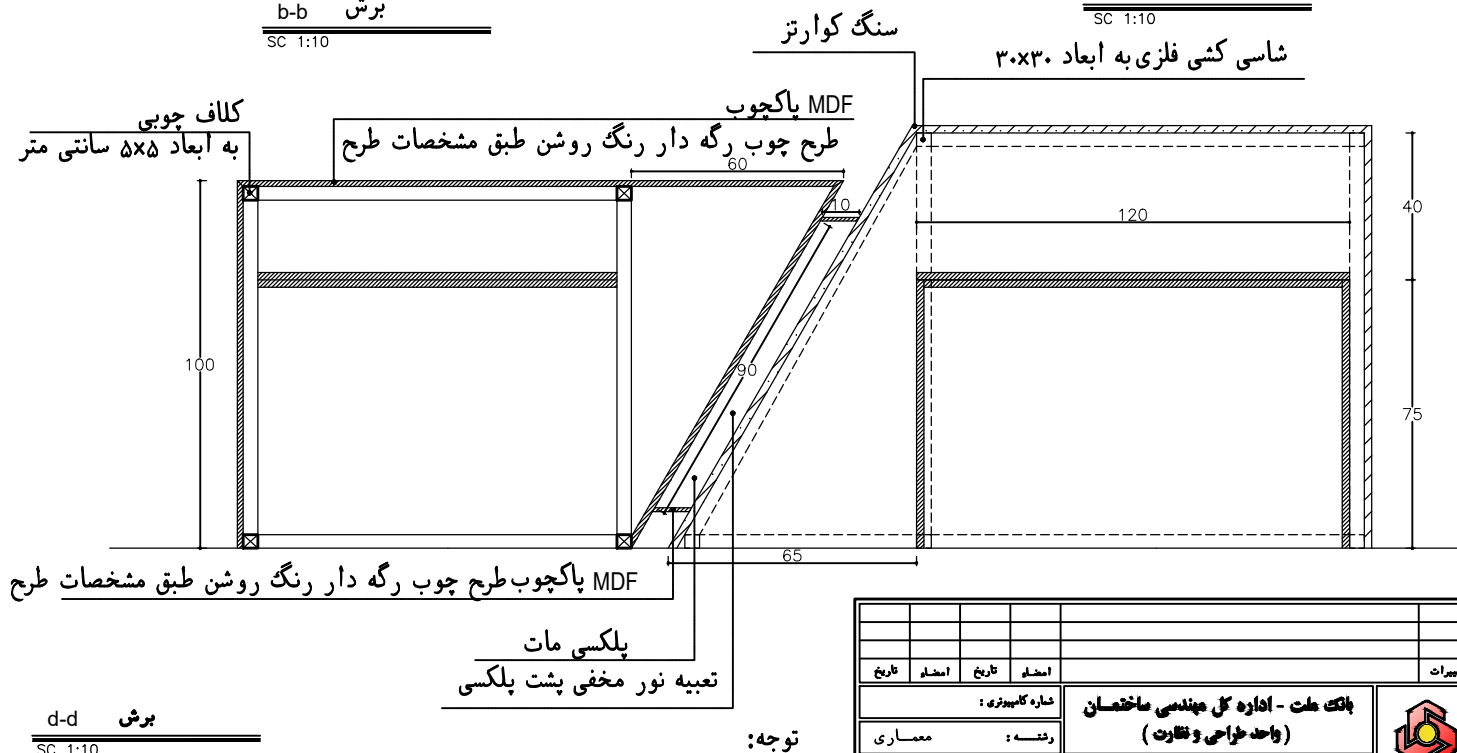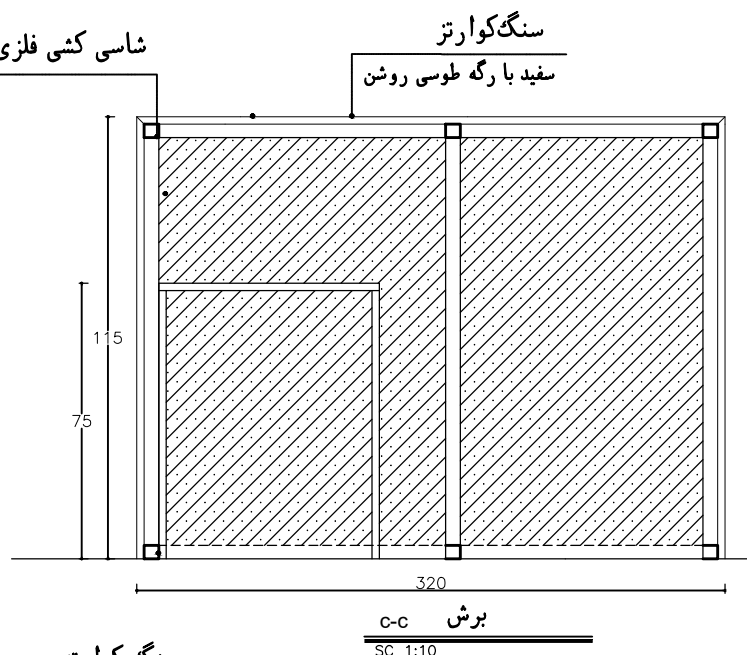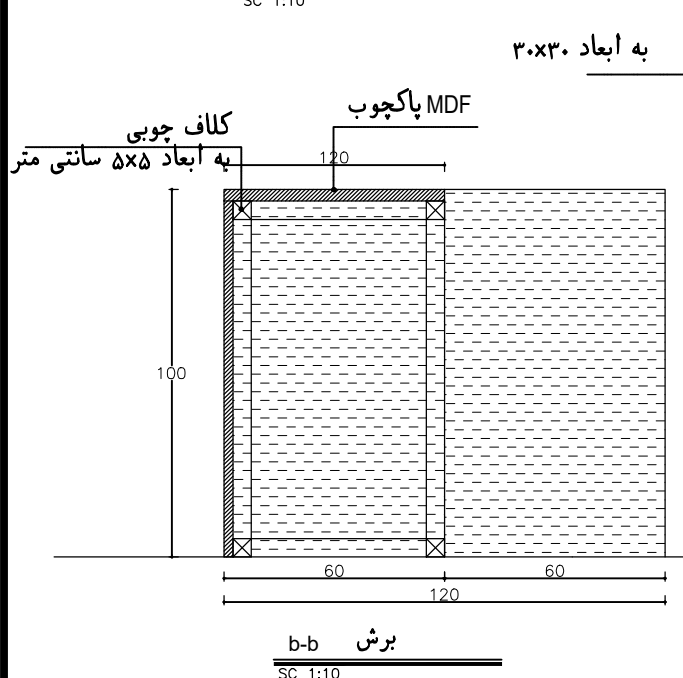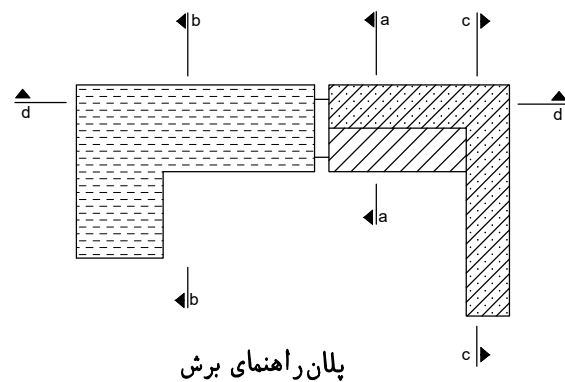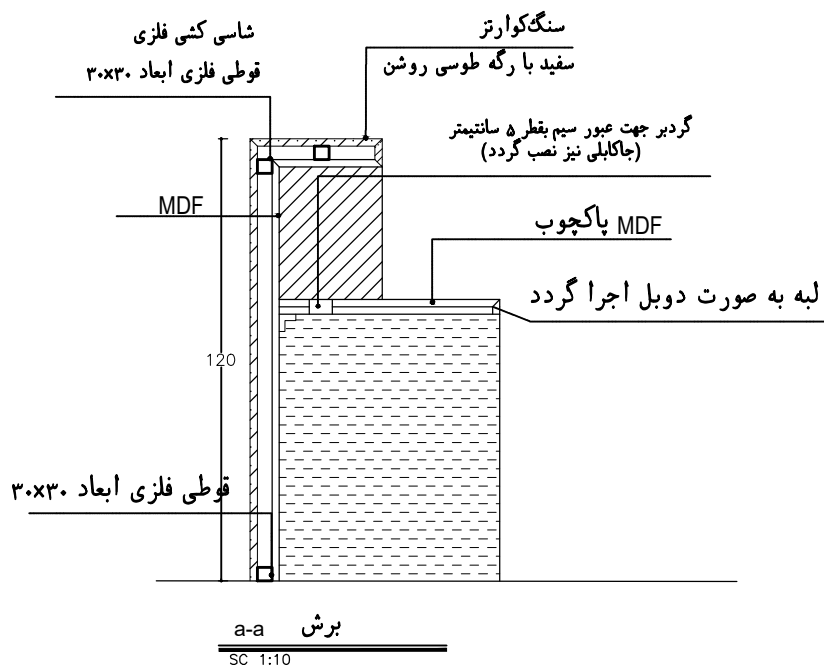



تغییرات		شماره کادربندی:	
تاریخ	امضاء	تاریخ	امضاء
پلانک هلت - اداره کل مهندسی ساختمان (واحد طراحی و نظارت)		عنوان پروژه: طبقه منفی یک ساختمان مرکزی فرصت	
معماری		عنوان نقشه: طراحی الی طبقه منفی یک فرصت	
تاریخ	امضاء	طراح	امضاء
۱۳۹۴/۴/۹	امیری زاده	ترسیم	امیری زاده
۱۳۹۴/۴/۹	امیری زاده	کنترل	
		تصویب	
شماره نقشه: A-08		شماره کادربندی: A-08	

توجه: پیمانکار موظف است قبل از اجرا اندازه های وضع موجود را برداشت کرده و با طرح تطبیق دهد.

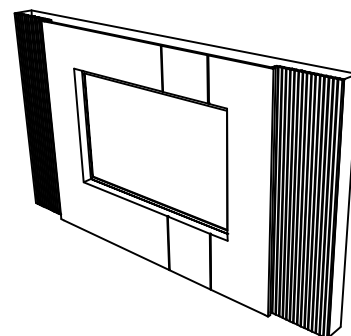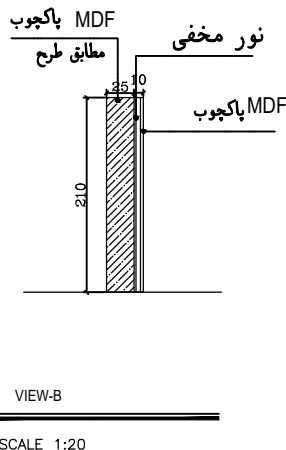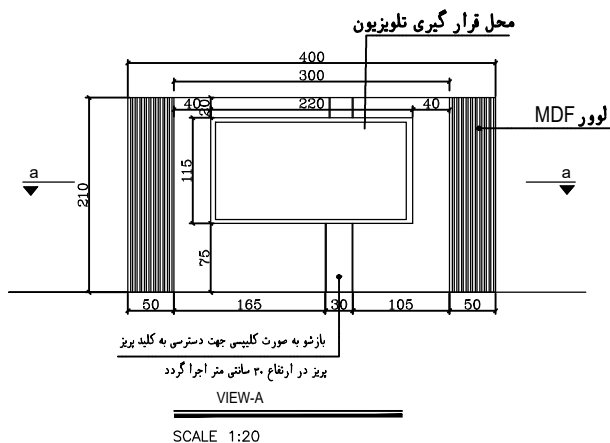

نمای سه بعدی استند تلویزیون

صرفاً به جهت درک بهتر طرح ارائه شده است
ملاك ابعاد و نقشه های دو بعدی خواهد بود.

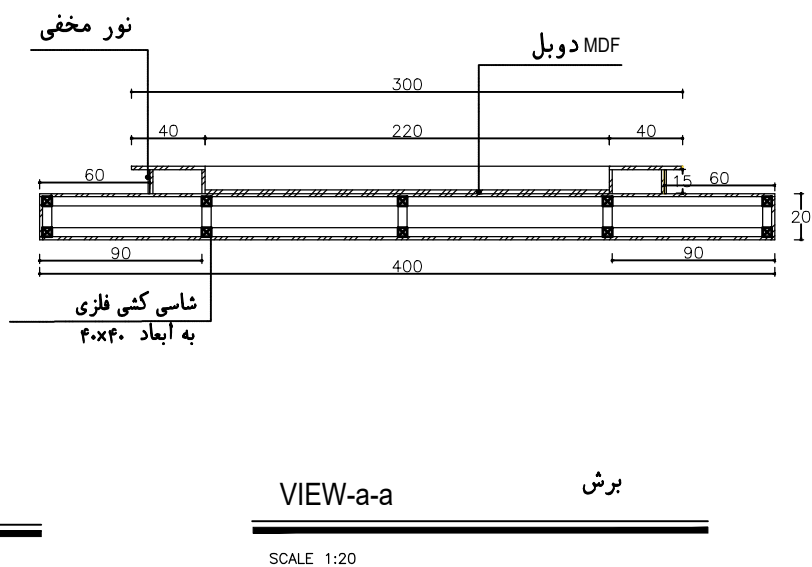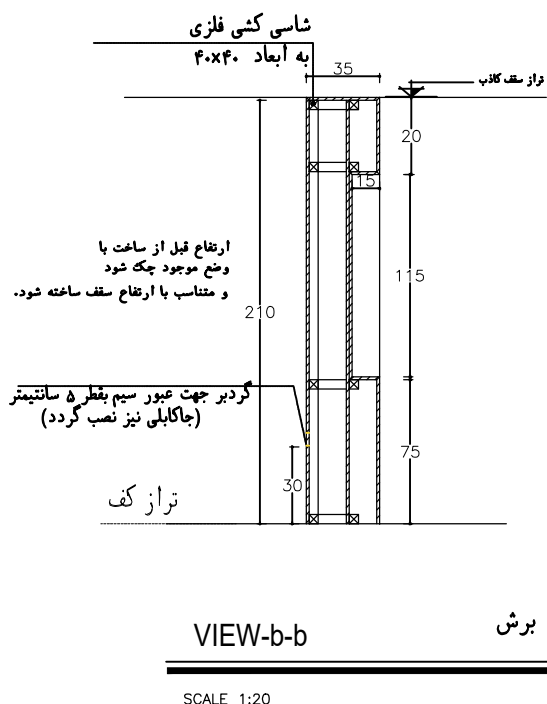


نکته:

استند نگهدارنده تلویزیون به سقف و کف فیکس شوند.


توجه:

پیمانکار موظف است قبل از اجرا اندازه های وضع موجود را برداشت کرده و با طرح تطبیق دهد.

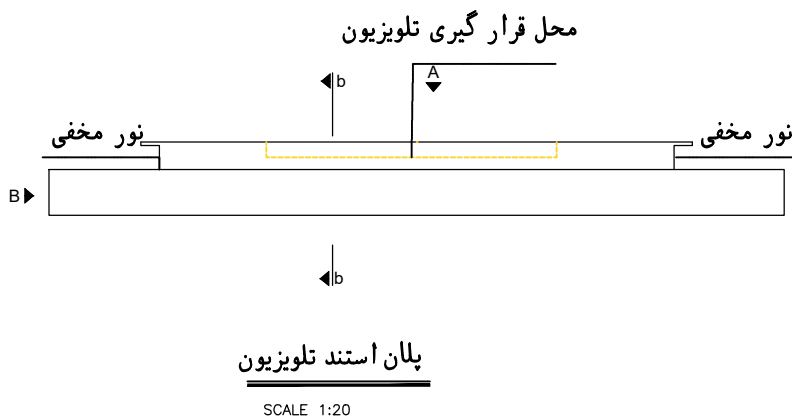


تاریخ		تاریخ		تاریخ	
مختار		مختار		مختار	
شماره کادربندی:		شماره کادربندی:		شماره کادربندی:	
معماری		معماری		معماری	
تاریخ		تاریخ		تاریخ	
۱۳۹۴/۴/۹		۱۳۹۴/۴/۹		۱۳۹۴/۴/۹	
امیر زاده		امیر زاده		امیر زاده	
توسعه		توسعه		توسعه	
کنترل		کنترل		کنترل	
تصویب		تصویب		تصویب	
عنوان نقشه:		عنوان نقشه:		عنوان نقشه:	
طراحی الی طبقه منفی یک فرصت		طراحی الی طبقه منفی یک فرصت		طراحی الی طبقه منفی یک فرصت	
عنوان نقشه:		عنوان نقشه:		عنوان نقشه:	
A-09		A-09		A-09	

پیمانکار موظف است قبل از اجرا نمونه تمامی متريال های مصرفی را به تایید طراح و ناظر برساند.

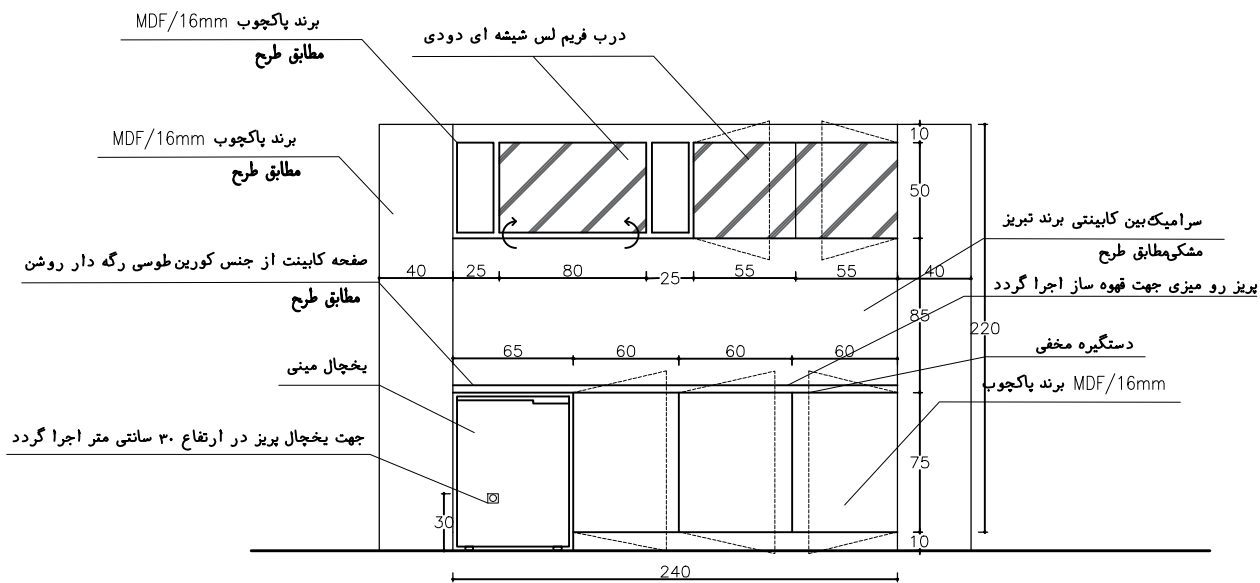


نما کابینت های فضای پذیرایی

SC 1:10

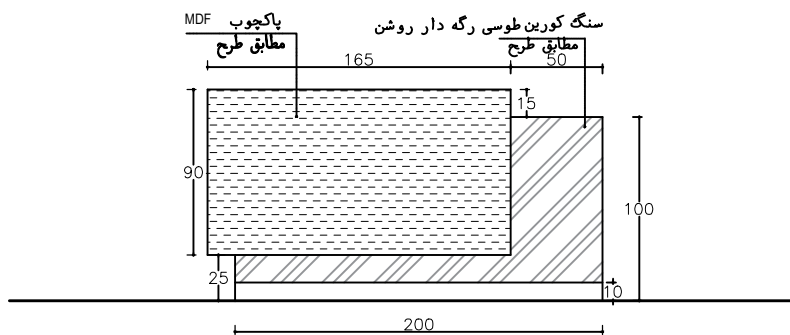

کانتربذیرایی


VIEW-A
SC 1:10

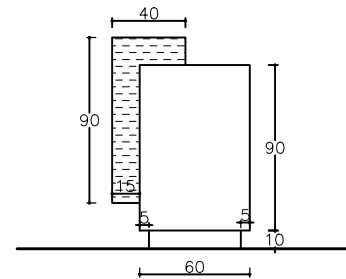

B کانتريڊيزاڻي

VIEW-B


SC 1:10

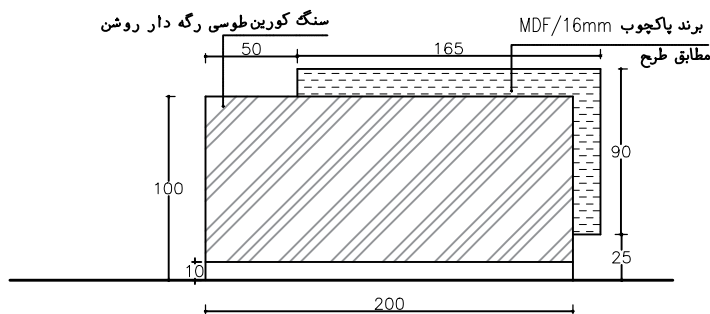

VIEW-C کانتریڈی رائی

VIEW-C

SC 1:10

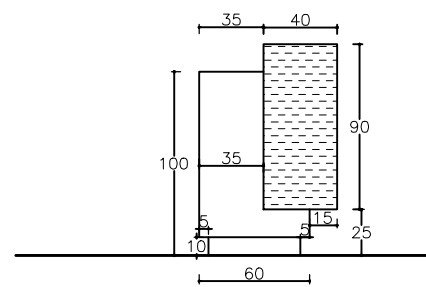

کانترپذیرایی


VIEW-D

SC 1:10

توجه:

پیمانکار موظف است قبل از اجرا اندازه های وضع موجود را برداشت کرده و با طرح تطبیق دهد.

پیمانکار موظف است قبل از اجرا نمونه تمامی متریا ل های مصرفی را به تایید طر ل و ناظر برساند.

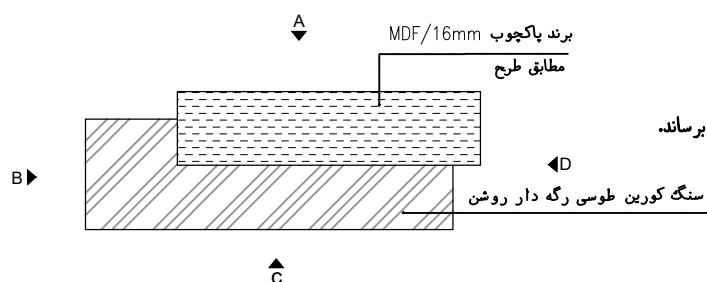


پلان کانتر پذیری

SC 1:10


[illegible]

سرامیک برند PMA مطابق طرح با تایید طرح و ناظر

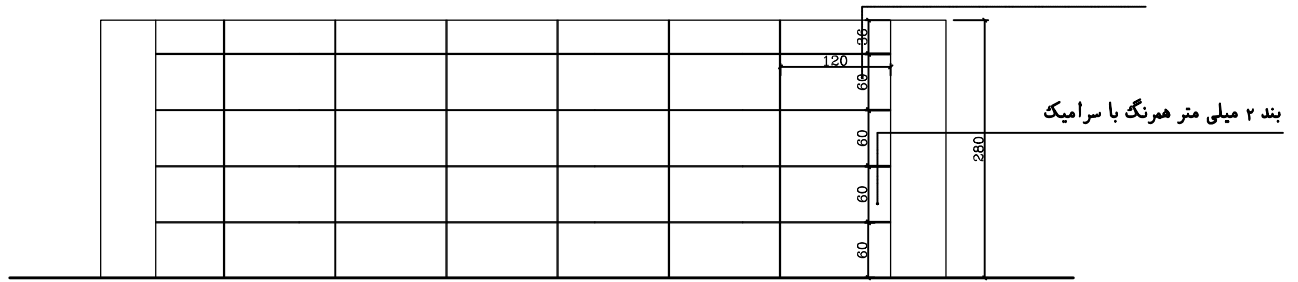

زیر سازی دیوار آبنما


SCALE 1:20

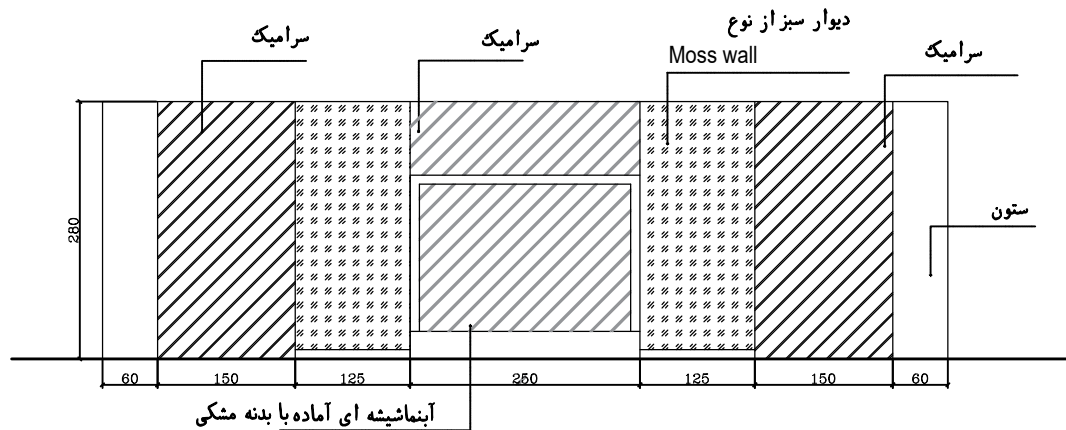

آبنماشیشه ای آماده با بدنه مشکی

نما دیوار آبنما

SCALE 1:20

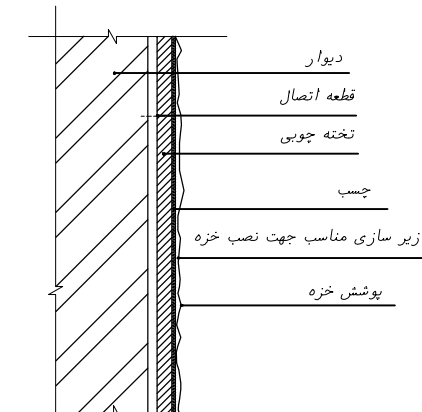

جزئیات اجرایی Moss wall

SCALE 1:10


توجه:

پیمانکار موظف است قبل از اجرا اندازه های وضع موجود را برداشت کرده و با طرح تطبیق دهد.

خرید و نصب آبنما مدل شیشه ای به ابعاد ۲۴۲٫۵ متر به عهده پیمانکار میباشد.

خرید و نصب ماس وال به عهده پیمانکار میباشد.

پیمانکار موظف است قبل از اجرا نمونه تمامی متريال های مصرفی را به تایید طراح و ناظر پروژه برساند.

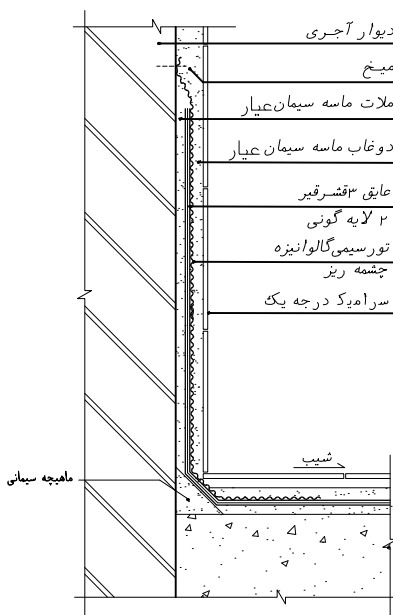

جزئیات اجرایی دیوار در مجاورت سطوح مرطوب

SCALE 1:10

تأیید		تأیید		تأیید	
تاریخ	امضاء	تاریخ	امضاء	تاریخ	امضاء
شماره کلامبربری:					
دفتر: معماری					
تاریخ	امضاء	طراح	امضاء	عنوان پروژه: طبقه منفی یک ساختمان مرکزی فرصت	
۱۴۰۴/۰۸	امیری زاده	ترسیم	امیری زاده	عنوان نقشه: طراحی الی طبقه منفی یک فرصت	
۱۴۰۴/۰۹	کنترل	تصویب		طراحی الی طبقه منفی یک فرصت	شماره نقشه: A-11

جدول نازک‌کاری

ردیف	شرح فضا	پوشش نهائی گس سازی	پوشش نهائی بالای ازاره دیوار	پوشش نهائی بالای ازاره دیوار	رنگ آمیزی دیوار	سقف اصلی	سقف گالوپ	رنگ آمیزی سقف	یاد آوری
①	ورودی	حفظ وضع موجود سرامیک و تمویض موکت موجود با موکت درجه یک برند ترک	قرنیز پی وی سی به رنگ ذغالی به ارتفاع ۱۰ سانتی متر	مطابق جزئیات دیوار ها	_____	_____	حفظ وضع موجود + ترمیم و رنگ آمیزی	رنگ پلاستیک پارس بهار کدرنگ ۴۱۰	_____
②	پذیرش	حفظ وضع موجود سرامیک و تمویض موکت موجود با موکت درجه یک برند ترک	قرنیز پی وی سی به رنگ ذغالی به ارتفاع ۱۰ سانتی متر	مطابق جزئیات دیوار ها	_____	_____	حفظ وضع موجود + ترمیم و رنگ آمیزی	رنگ پلاستیک پارس بهار کدرنگ ۴۱۰	_____
③	فضای انتظار	حفظ وضع موجود سرامیک و تمویض موکت موجود با موکت درجه یک برند ترک	قرنیز پی وی سی به رنگ ذغالی به ارتفاع ۱۰ سانتی متر	مطابق جزئیات دیوار ها	_____	_____	حفظ وضع موجود + ترمیم و رنگ آمیزی	رنگ پلاستیک پارس بهار کدرنگ ۴۱۰	_____
④	دیوار E,F	_____	قرنیز پی وی سی به رنگ ذغالی به ارتفاع ۱۰ سانتی متر	کاغذ دیواری درجه یک به رنگ طوسی روشن	_____	_____	_____	_____	_____
⑤	دیوار A,B	_____	قرنیز پی وی سی به رنگ ذغالی به ارتفاع ۱۰ سانتی متر	لمسه کوبی پارچه مخمل و استیل مطابق جزئیات دیوار ها	_____	_____	_____	_____	_____
⑥	دیوار D,C	_____	قرنیز پی وی سی به رنگ ذغالی به ارتفاع ۱۰ سانتی متر	مطابق جزئیات دیوار ها	_____	_____	_____	_____	_____
⑦	فضای آسانسور	_____	قرنیز پی وی سی به رنگ ذغالی به ارتفاع ۱۰ سانتی متر	مطابق جزئیات دیوار ها	_____	_____	_____	_____	_____

توجه:

ساخت باغچه ترئینی با U چوبی MDF پاکچوب به رنگ مشکی مات (به ضلع ۱۰ سانتی متر)
کف باغچه چمن مصنوعی اجرا گردد و با سنگ رودخانه ای سفید پر گردد.

توجه:

جهت تلویزیون و یخچال و دستگاه قهوه ساز و آبما پریز برق با سرخط مجزا از تابلوی برق در نظر گرفته شود.

پیمانکار موظف است قبل از اجرا اندازه های وضع موجود را

برداشت کرده و با طرح تطبیق دهد.

چراغ خطی با عرض ۶ سانتی متر در محل های مشخص شده اجرا گردد.


یاد آوری:

-کلیه مصالح مصرفی از نوع مرغوب می باشد.

کلیه ابعاد قبل از ساخت با وضع موجود چک شود.

کلیه MDF مصرفی از برند پاکچوب باشد و قبل از اجرا به تایید طراح و ناظر پروژه برسد

در صورت عدم موجودی مصالح موجود در جدول نازککاری پیمانکار موظف است نسبت به تهیه و اجرای مصالح مشابه با هماهنگی و تایید ناظر پروژه اقدام نماید.

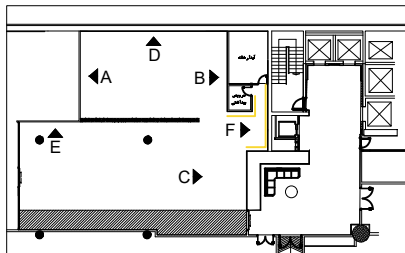

پلان راهنما

چک هت - اداره کل مهندسی ساختمان (واحد طراحی و نظارت)		ابعاد فضا: 42.00x29.70cm ردیف: _____ مصارف: _____	
عنوان پروژه: جدول نازککاری		تاریخ: ۱۴۰۴/۰۹/۰۹ اسم: امیری زاده طراح: امیری زاده	مهندس: _____ طراح: _____
عنوان نقشه: طراحی ایلی طبقه منفی یک فرست		تاریخ: ۱۴۰۴/۰۹/۰۹ اسم: امیری زاده طراح: امیری زاده	مهندس: _____ طراح: _____



شماره نقشه: A-12