



بسمه تعالی

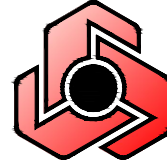

بانک ملت - اداره کل مهندسی ساختمان (واحد طراحی و نظارت)

عنوان پروژه : لابی منفی فرصت

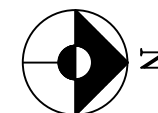


تاریخ	امضاء	تاریخ	امضاء						مهرات
شماره کپیورتری :				بناکت ملت - اداره کل مهندسی ساختمان (واحد طراحی و نظارت) 					
رشته:									
معماری									
تاریخ	امضاء	طراح	فرسهم	عنوان پروژه : طبقه منفی یک ساختمان مرکزی فرصت					
۱۳۹۶٫۰۹	امیری زاده								
۱۳۹۶٫۰۹	امیری زاده			عنوان نقشه : طرح ای لابی طبقه منفی یک فرصت					
		کنترل	مصوب						

پیمانکار موظف است قبل از اجرا اندازه های وضع موجود را برداشت کرده و با طرح تطبیق دهد.

sc 1.100

مساحت ۴۰۰ متر مربع

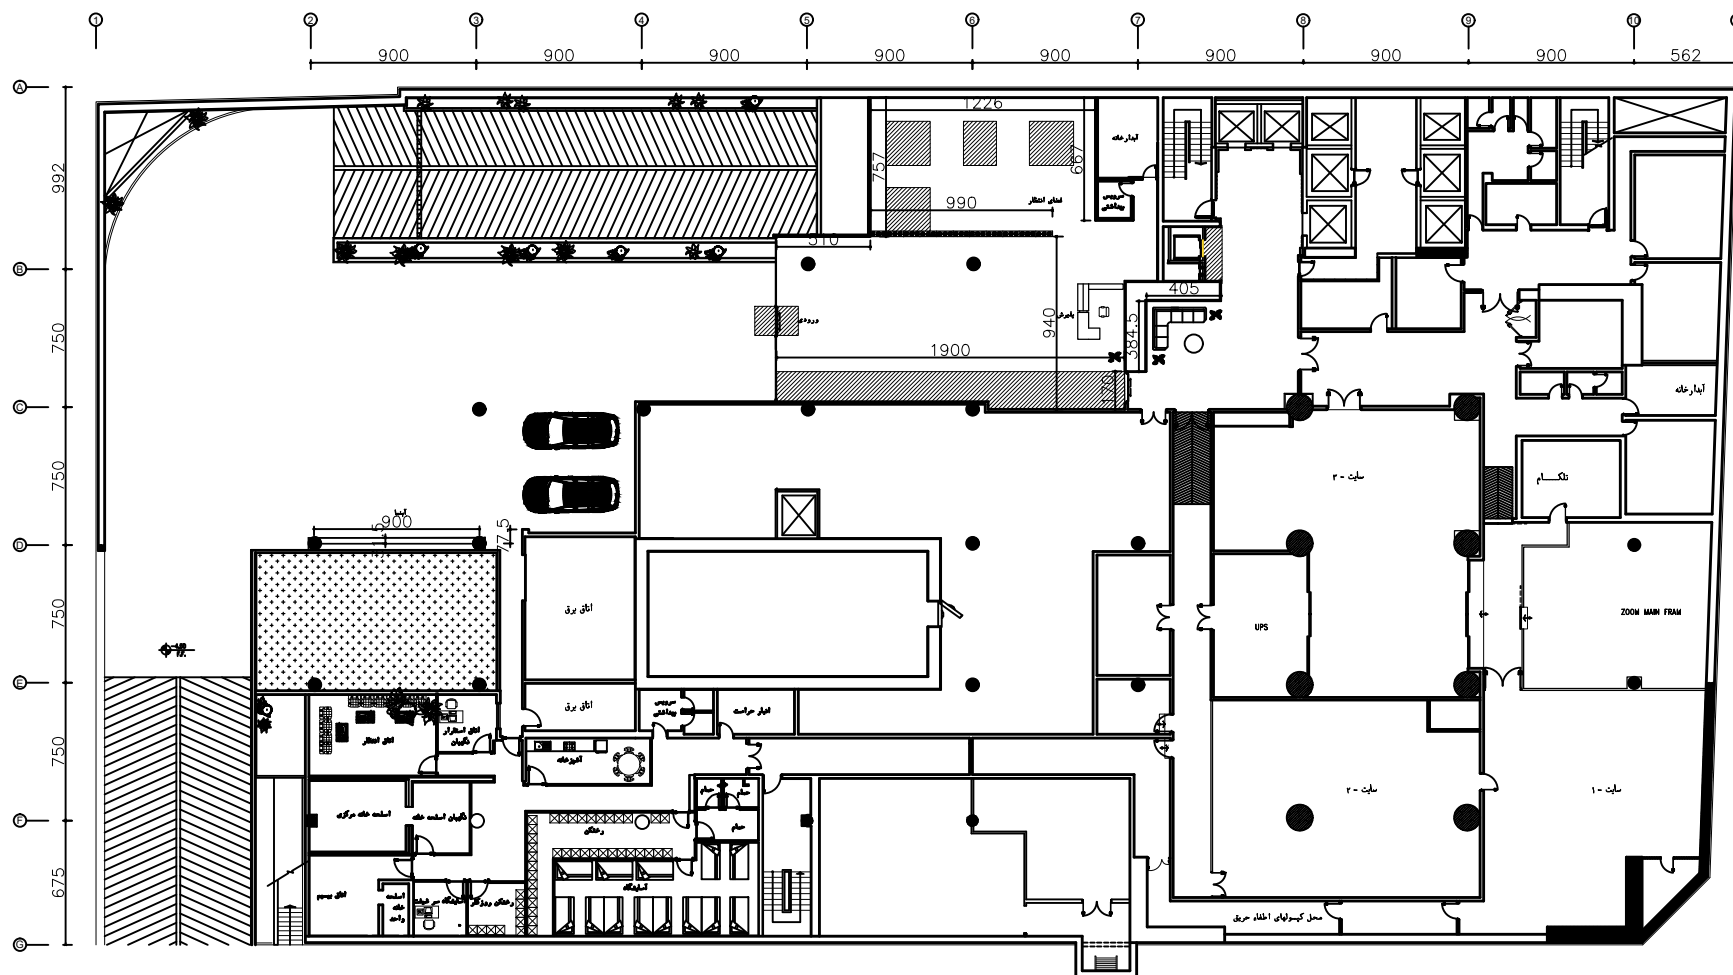


پلان اندازه گذاری

مساحت ۴۰۰ متر مربع sc 1:100

توجه:

پیمانکار موظف است قبل از اجرا اندازه های وضع موجود را برداشت کرده و با طرح تطبیق دهد.

تاییدات		امضاء		تاریخ	
شماره کاپیویری:		معماری		تاریخ	
پانک ملت - اداره کل مهندسی ساختمان (واحد طراحی و نظارت)		رقشه:		تاریخ	
عنوان پروژه: طبقه منفی یک ساختمان مرکزی فرصت		طراح:		تاریخ	
مهندس: طبق نقشه		ترسیم:		تاریخ	
عنوان نقشه: طراحی لابی طبقه منفی یک فرصت		کنترل:		تاریخ	
شماره نقشه: A-02		تصویب:		تاریخ	

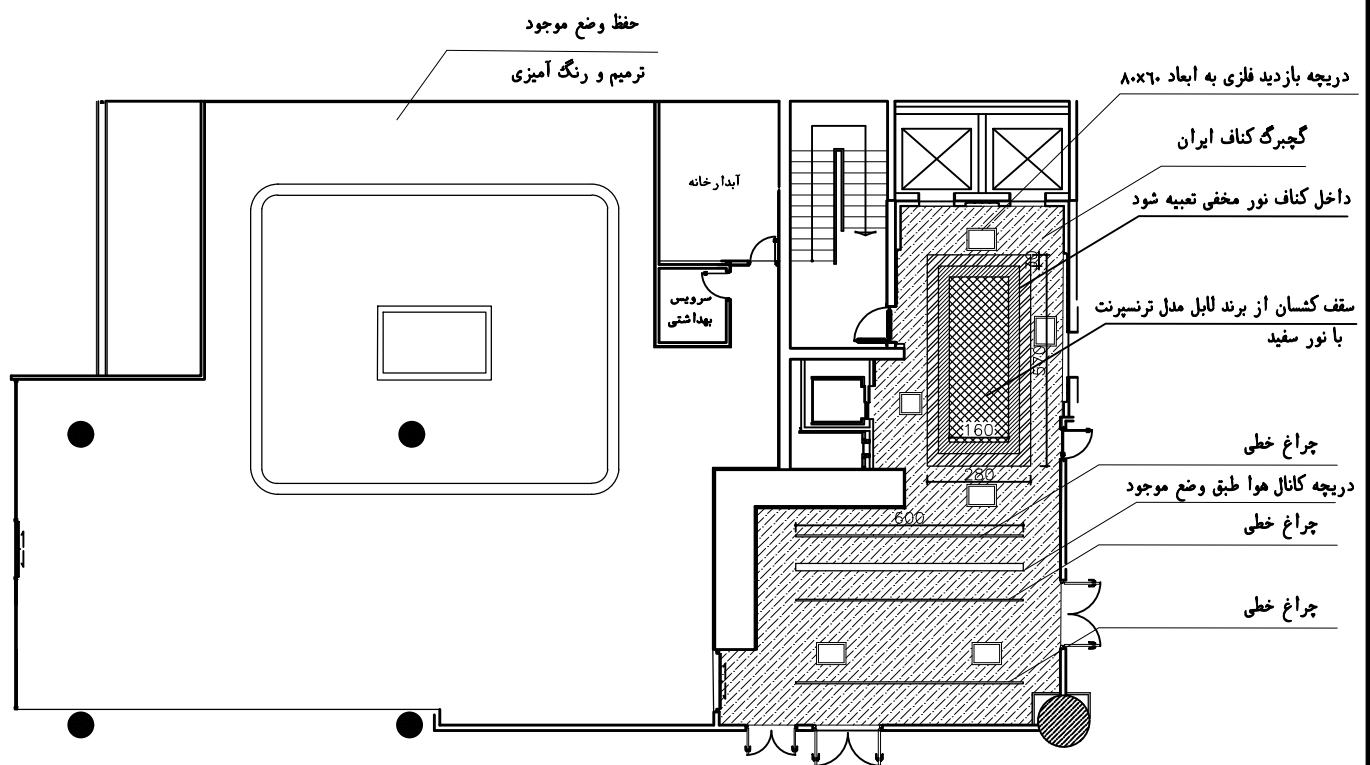


پلان سقف کاذب
مساحت ۴۰۰ متر مربع
sc 1.50


- ۲۳۳+ از کف تمام شده (وضع موجود)
- ۲۷۰+ از کف تمام شده (وضع موجود)
- ۲۶۰+ از کف تمام شده (وضع موجود)
- ۲۶۰+ از کف تمام شده (وضع موجود)

توجه:

پیمانکار موظف است قبل از اجرا اندازه های وضع موجود را برداشت کرده و با طرح تطبیق دهد.

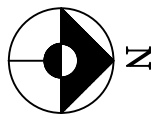


تجهیزات		شماره کادربندی:	
بانک ملت - اداره کل مهندسی ساختمان (واحد طراحی و نظارت)		معماری	
عنوان پروژه: طبقه منفی یک ساختمان مرکزی فرصت		معماری	
عنوان نقشه: طراحی لابی طبقه منفی یک فرصت		معماری	
طراحی: طایفه		معماری	
شماره نقشه: A-03		معماری	
تاریخ		امضاء	
۱۳۹۴/۴/۹		امیری زاده	
۱۳۹۴/۴/۹		امیری زاده	
تصویر		تصویر	

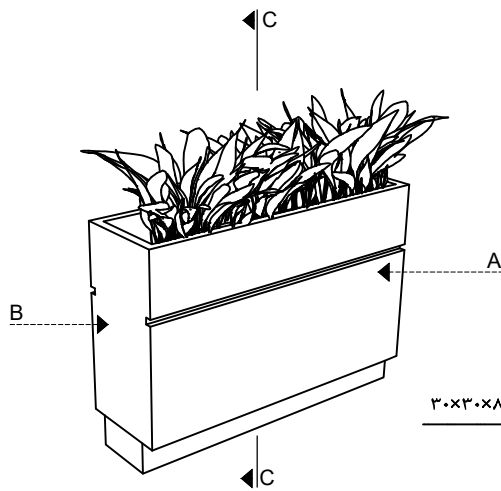

نمای سه بعدی


صرفاً به جهت درک بهتر طرح ارائه شده است
ملاک ابعاد و نقشه های دو بعدی خواهد بود.

گلدان پلاستیکی به ابعاد ۳۰×۳۰×۸۰

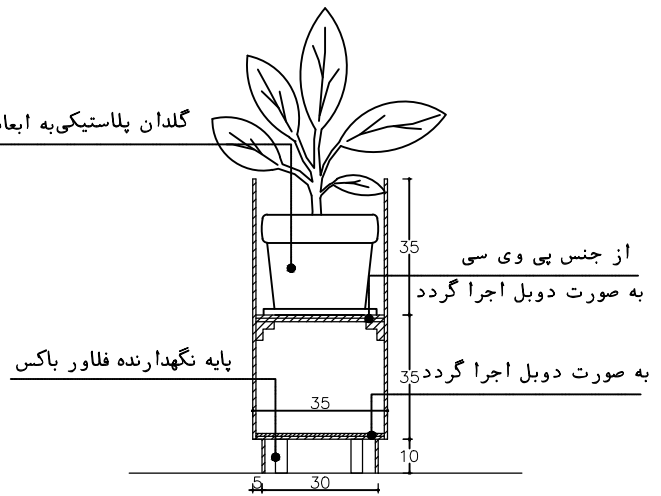


مقطع فلاور باکس C-C

SC 1:5

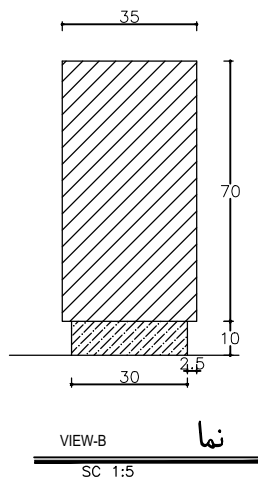

SC 1:5

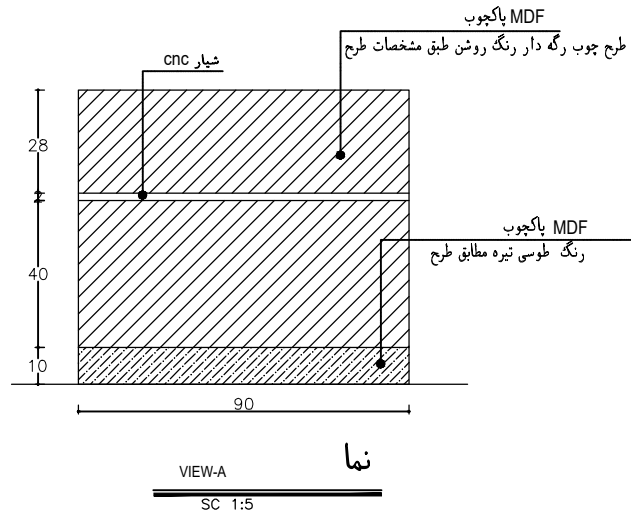


SC 1:5


توجه:

پیمانکار موظف است قبل از اجرا اندازه های وضع موجود را
برداشت کرده و با طرح تطبیق دهد.


تغییرات		شماره کلامبرتری:	
تاریخ	امضاء	تاریخ	امضاء
پانک ملت - اداره کل مهندسی ساختمان (واحد طراحی و نظارت)		عنوان پروژه: طبقه منفی یک ساختمان مرکزی فرصت	
معماری		عنوان نقشه: طراحی لابی طبقه منفی یک فرصت	
تاریخ	امضاء	طراح	امضاء
۱۳۹۴/۴/۹	امیری زاده	ترسیم	امیری زاده
۱۳۹۴/۴/۹	امیری زاده	کنترل	
		تصویب	
مهندس: طبق نقشه		شماره نقشه: A-04	

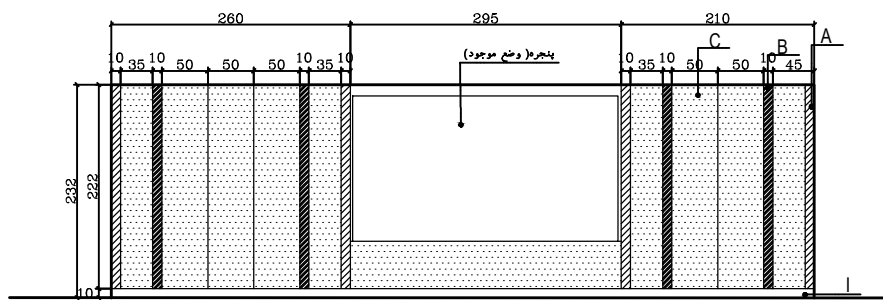


VIEW-A
SCALE 1:20

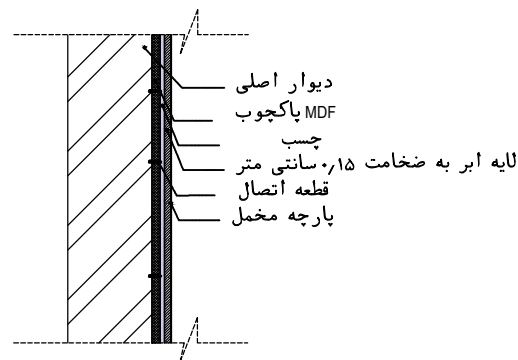

مقطع دیوار لمسه کوبی
SC 1:5

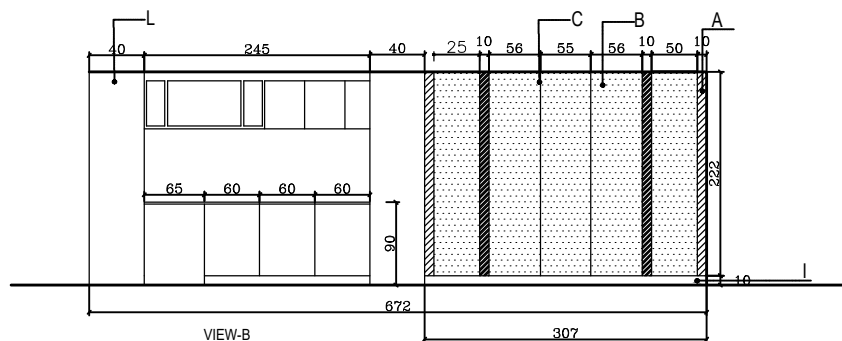


VIEW-B
SCALE 1:20

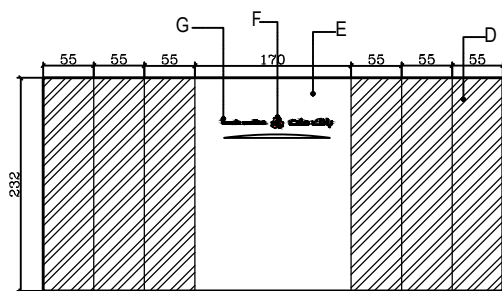

VIEW-C
SC 1:20


کد	م مصالح	رنگ	کد رنگ
A	نوار استیل	طلایی	
B	نوار استیل	دودی براق	
C	پارچه لمسه کوبی	طوسی کرم روشن	مدل دیاموند پالس ۱۰
D	MDF پاکچوب	رنگه دار روشن	طبق طرح
E	سرامیک برند pma یوک میچ	مطابق طرح	به ابعاد ۲۸×۱۲۰
F	لوگوی بانک از پلکسی گلاس ضخامت ۶ میلیمتر (لوگو فریم مطابق طرح و رنگ سازمانی)	نارنجی	RAL Code: 1028
G	لوگو نوشته بانک از پلکسی گلاس ضخامت ۶ میلیمتر	قرمز	RAL Code: 3020
		سفید	RAL Code: 9016
I	فرنیز پی وی سی	خاکستری تیره	
L	کابینت بالبرایی مطابق جزئیات		
M	لاکوبل مشکی حفظ وضع موجود		

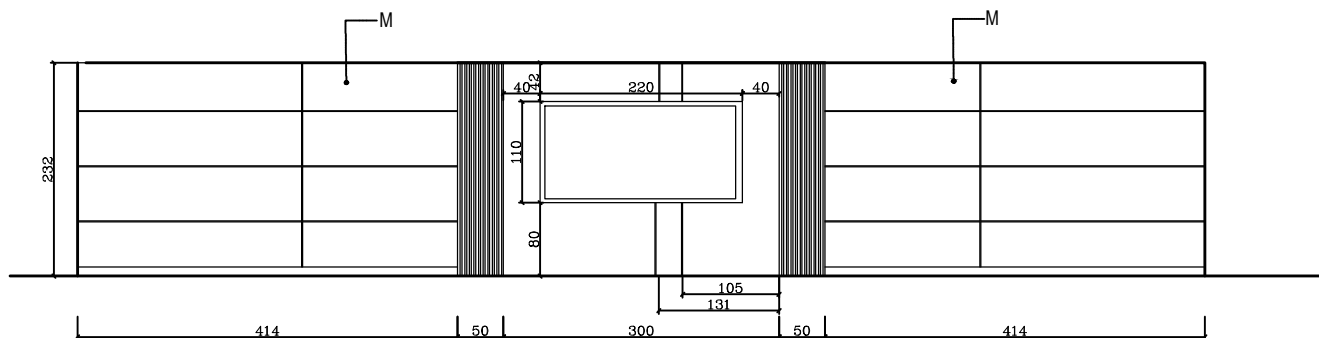

VIEW-D
SC 1:20

توجه:


پیمانکار موظف است قبل از اجرا نمونه تمامی متریال های مصرفی را به تایید طراح و ناظر پروژه برساند.
پیمانکار موظف است قبل از اجرا اندازه های وضع موجود را برداشت کرده و با طرح تطبیق دهد.

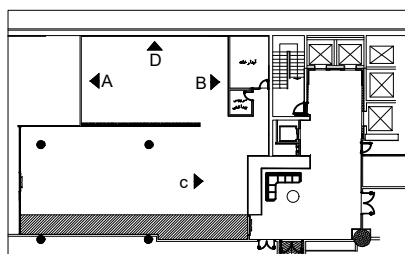

پلان رامنا



تغییرات	تاریخ	امضاء	تاریخ	امضاء
شماره کادربندی:				
بانک ملت - اداره کل مهندسی ساختمان (واحد طراحی و نظارت)				
عنوان پروژه: طبقه منفی یک ساختمان مرکزی فرصت				
عنوان نقشه: طراحی لابی طبقه منفی یک فرصت				
شماره نقشه: A-05				
طراحی: طراح				
تصویر: تصویر				
تاریخ: ۱۳۹۴/۰۹/۰۹				
امضاء: امیری زاده				
تاریخ: ۱۳۹۴/۰۹/۰۹				
امضاء: امیری زاده				



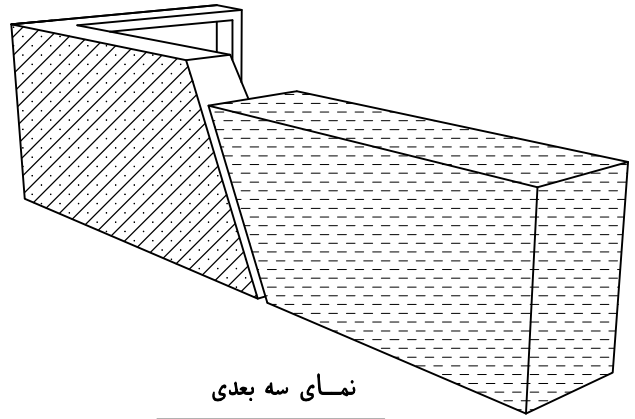


نمای سه بعدی

مرا به جهت درگ بهتر طرح ارائه شده است
ملاک ابعاد و نقشه های دو بدی خواهد بود.

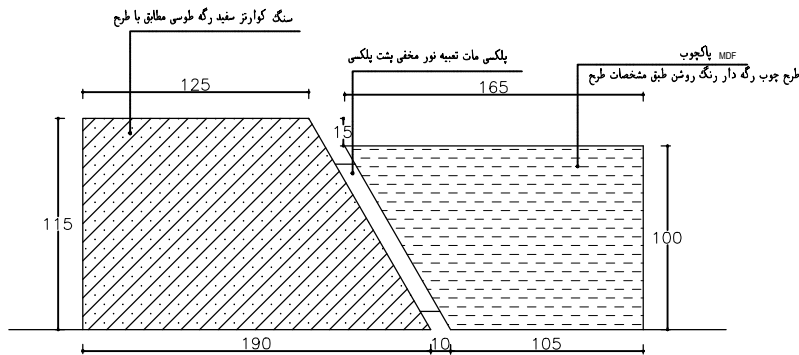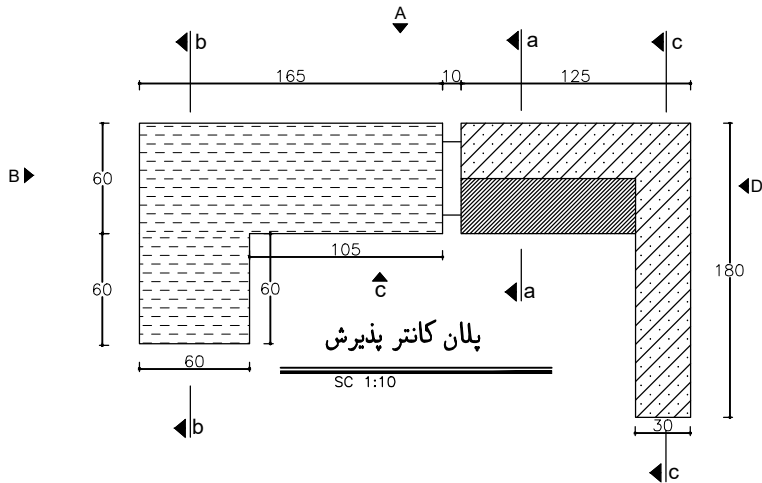


نمای کانتر پذیرش
SC 1:10

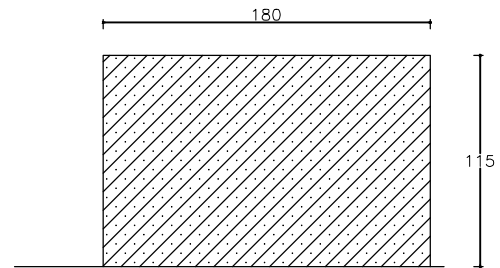

VIEW-D
SC 1:10


لبه ها به صورت دابل اجرا گردد (۱۰ سانتی متر برگشت)

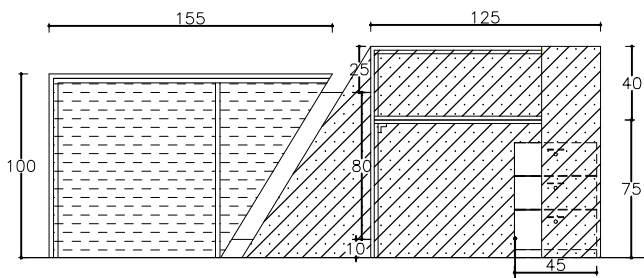

VIEW-C

SC 1:10

پوینت متحرک از نوع متریال کانتر و تمیبه قل برای تمام کتوها
(دستگیره به طول ۱۰ سانتیمتر از استیل مات غش دار)

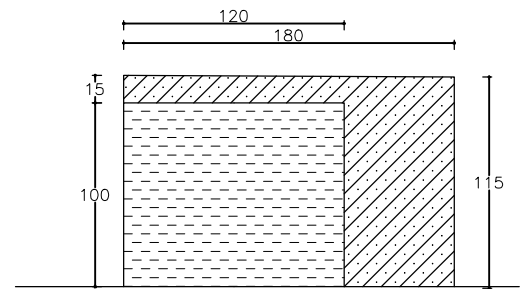

VIEW-B







SC 1:10

توجه:




پیمانکار موظف است قبل از اجرا اندازه های وضع موجود را
برداشت کرده و با طرح تطبیق دهد.

پیمانکار موظف است قبل از اجرا نمونه تمامی متریال های مصرفی را به تایید طراح و ناظر برساند.

تاییدات		شماره کادربندی:	
امضاء	تاریخ	امضاء	تاریخ
پانک ملت - اداره کل مهندسی ساختمان (واحد طراحی و نظارت)		عنوان پروژه: طبقه منفی یک ساختمان مرکزی فرصت	
عنوان نقشه:		طراحی ایلی طبقه منفی یک فرصت	
تاریخ	امضاء	تاریخ	امضاء
۱۳۹۴/۴/۹	امیری زاده	۱۳۹۴/۴/۹	امیری زاده
۱۳۹۴/۴/۹	کنترل	۱۳۹۴/۴/۹	تصویب
شماره نقشه: A-07		طرح: طرح	

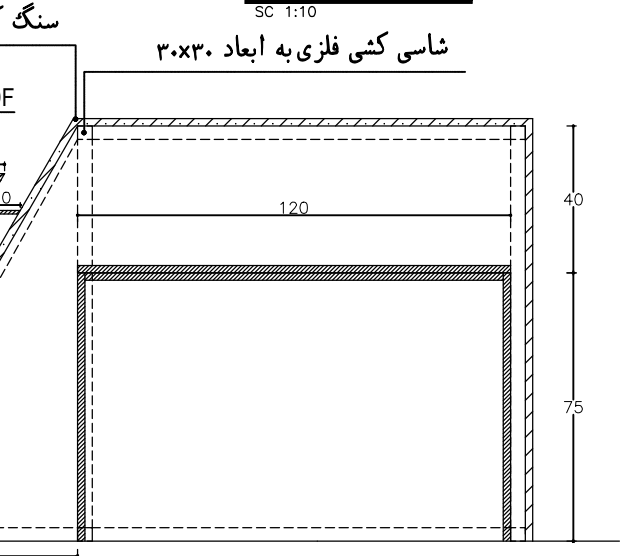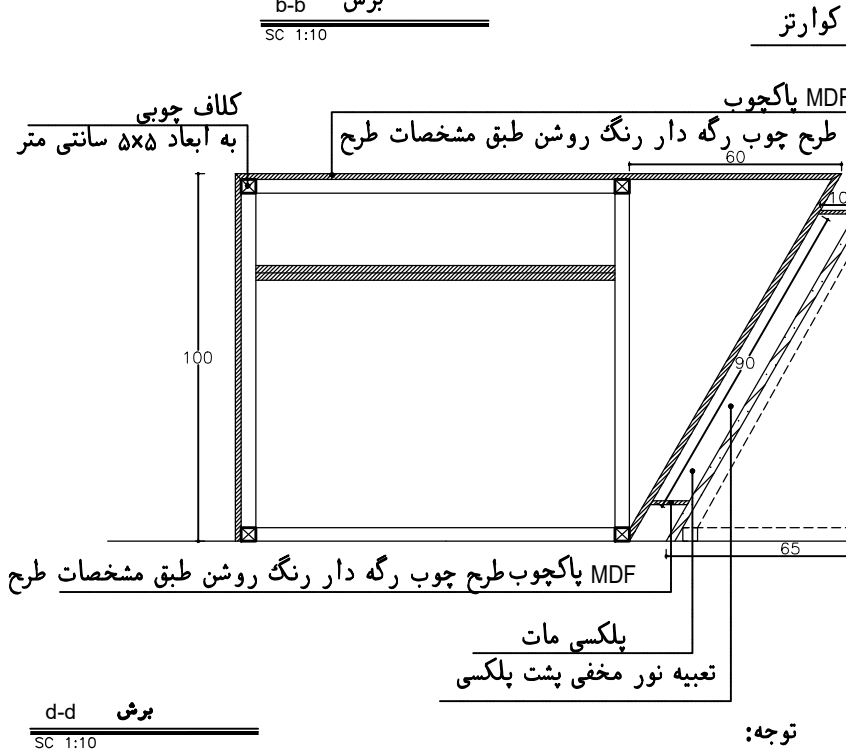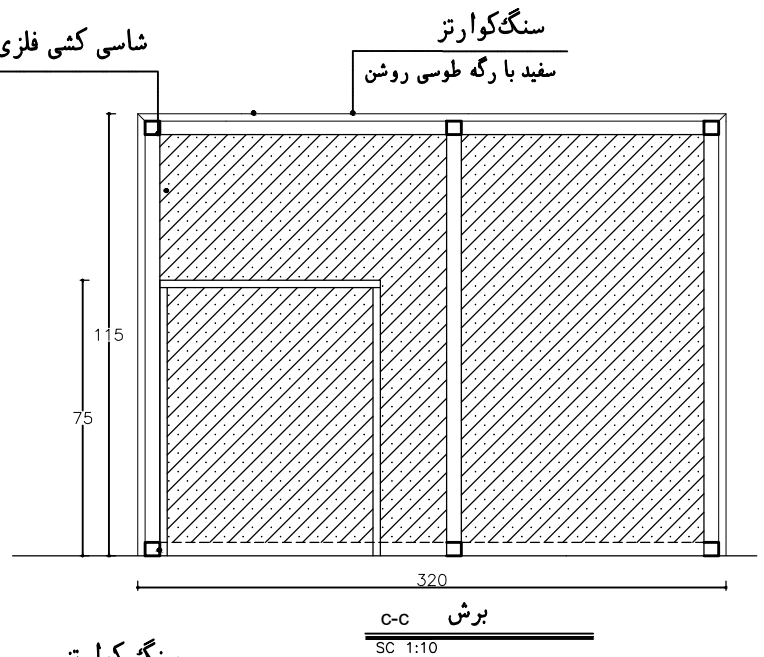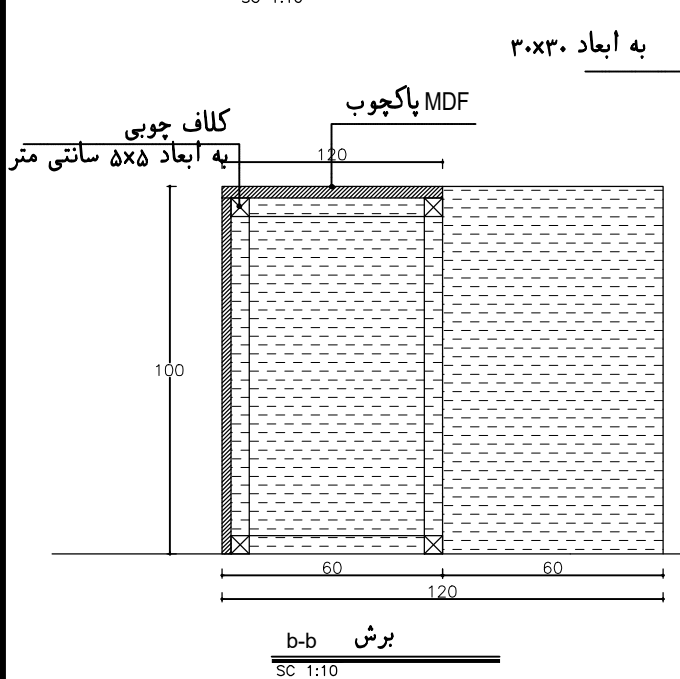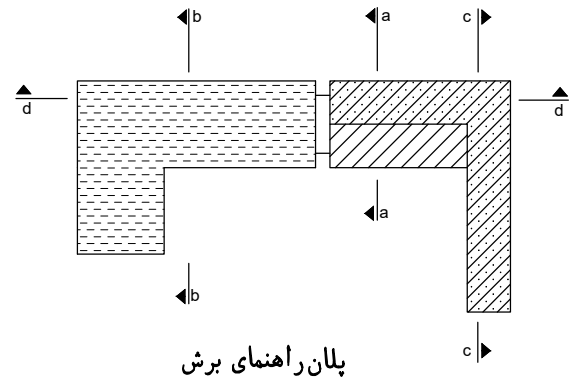
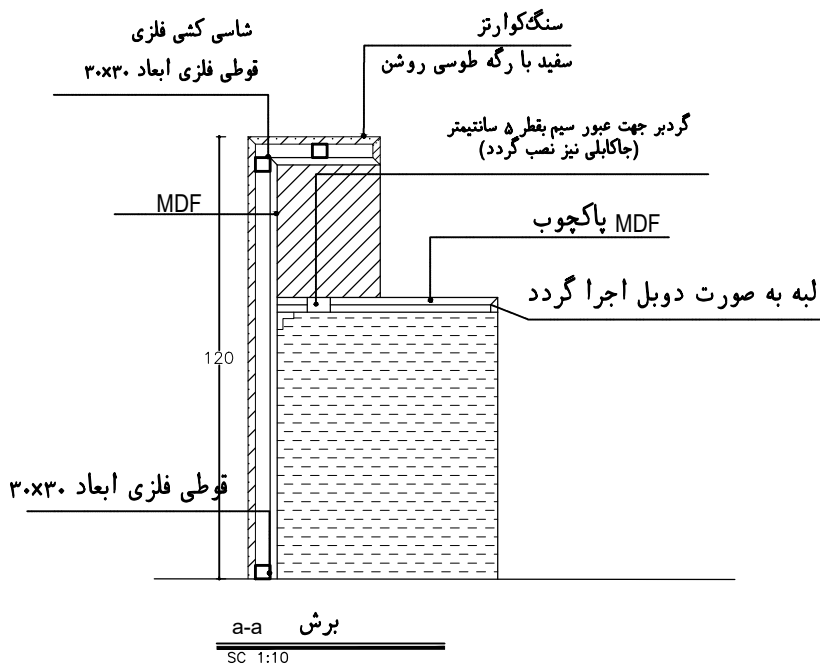


تغییرات		شماره کادربندی:	
تاریخ	امضاء	تاریخ	امضاء
پانک ملت - اداره کل مهندسی ساختمان (واحد طراحی و نظارت)		عنوان پروژه: طبقه منفی یک ساختمان مرکزی فرصت	
معماری		عنوان نقشه: طراحی لابی طبقه منفی یک فرصت	
تاریخ	امضاء	طراح	امضاء
۱۳۹۴/۴/۹	امیری زاده	ترسیم	امیری زاده
۱۳۹۴/۴/۹	امیری زاده	کنترل	
		تصویب	
طوبی: پیمانکار موظف است قبل از اجرا اندازه های وضع موجود را برداشت کرده و با طرح تطبیق دهد.		شماره نقشه: A-08	

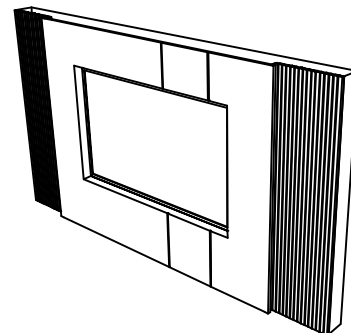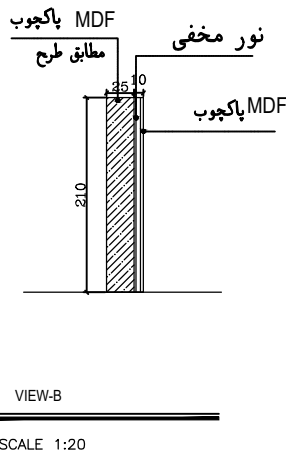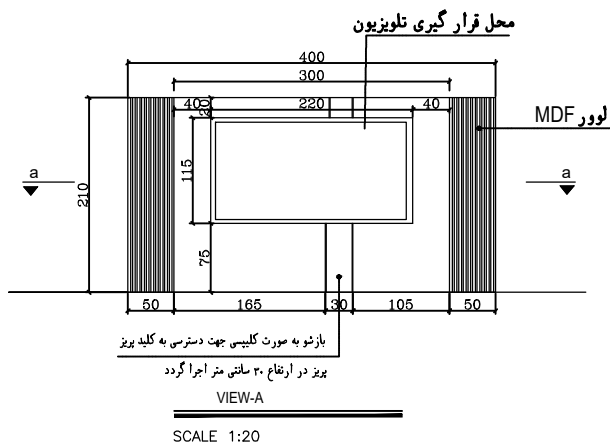

نمای سه بعدی استند تلویزیون

صرفاً به جهت درک بهتر طرح ارائه شده است
ملاك ابعاد و نقشه های دو بعدی خواهد بود.

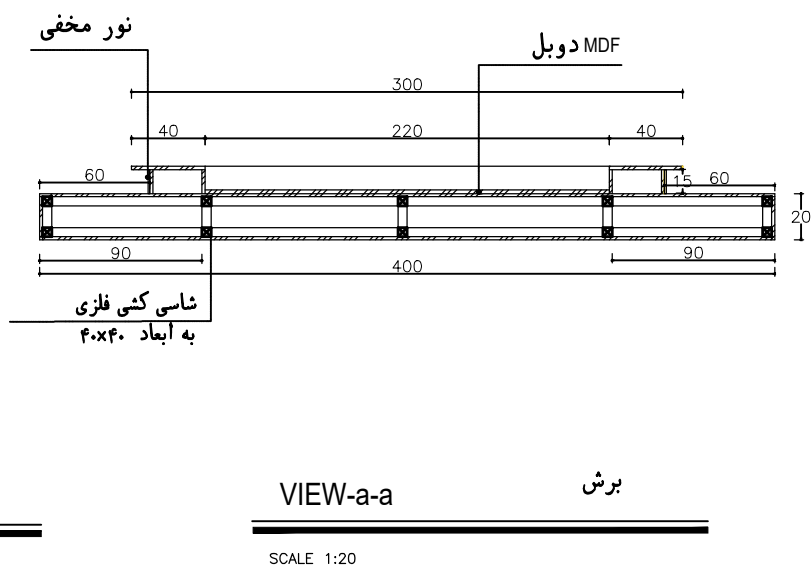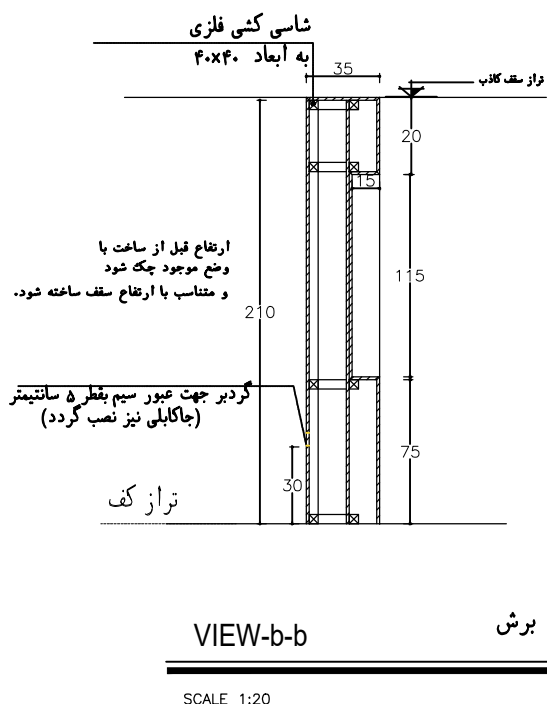


نکته:

استند نگهدارنده تلویزیون به سقف و کف فیکس شوند.


توجه:

پیمانکار موظف است قبل از اجرا اندازه های وضع موجود را
برداشت کرده و با طرح تطبیق دهد.

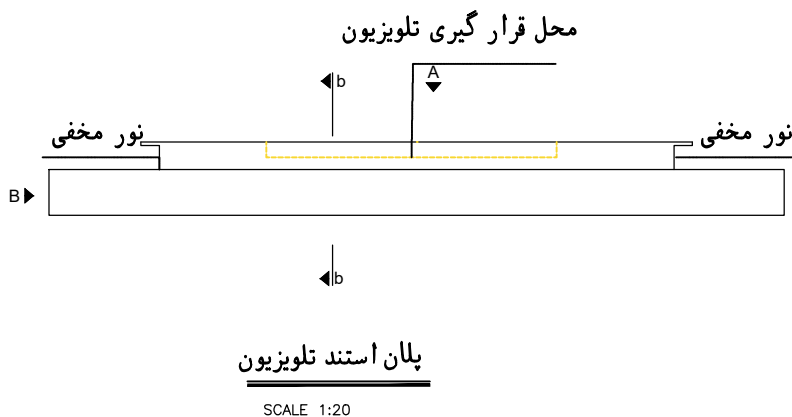


تاریخ		تاریخ		تاریخ	
مختار		مختار		مختار	
شماره کادربندی:		شماره کادربندی:		شماره کادربندی:	
معماری		معماری		معماری	
تاریخ		تاریخ		تاریخ	
۱۳۹۴/۴/۹		۱۳۹۴/۴/۹		۱۳۹۴/۴/۹	
امیر زاده		امیر زاده		امیر زاده	
توسعه		توسعه		توسعه	
کنترل		کنترل		کنترل	
تصویب		تصویب		تصویب	
عنوان نقشه:		عنوان نقشه:		عنوان نقشه:	
طراحی الی طبقه منفی یک فرصت		طراحی الی طبقه منفی یک فرصت		طراحی الی طبقه منفی یک فرصت	
عنوان نقشه:		عنوان نقشه:		عنوان نقشه:	
A-09		A-09		A-09	

پیمانکار موظف است قبل از اجرا نمونه تمامی متريال های مصرفی را به تایید طراح و ناظر برساند.

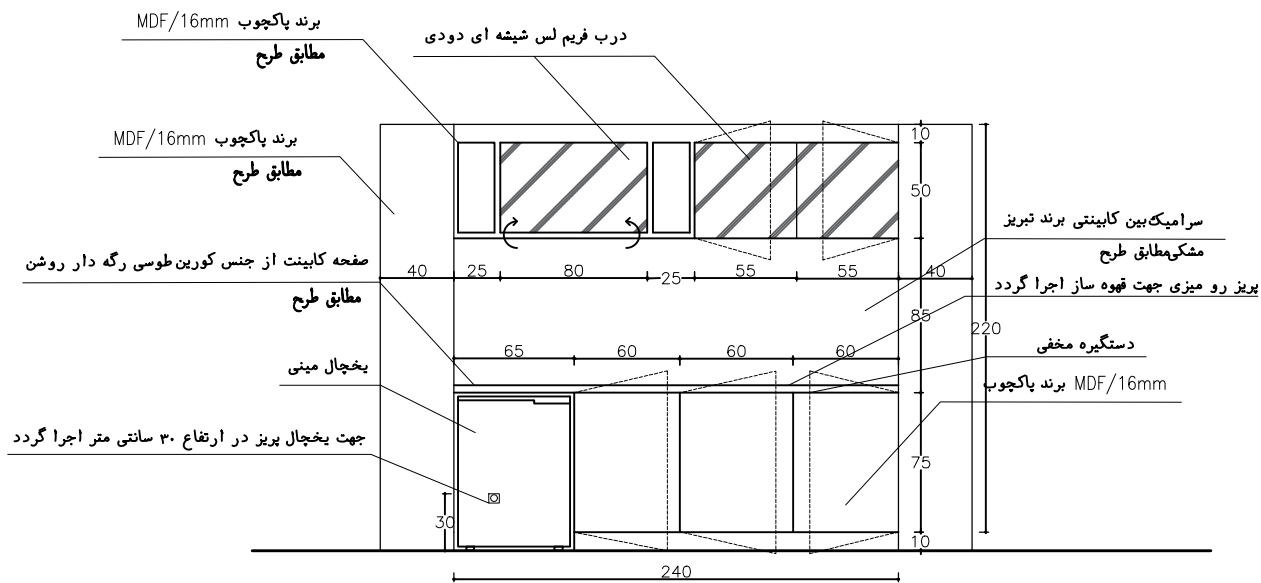


نما کابینت های فضای پذیرایی

SC 1:10

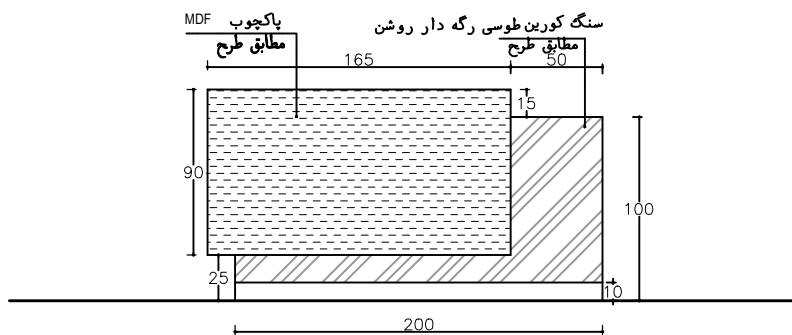


کانتر پذیرایی

VIEW-A
SC 1:10

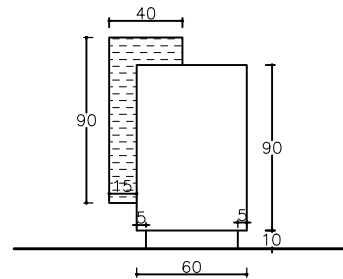


کانتر پذیرایی

VIEW-B
SC 1:10

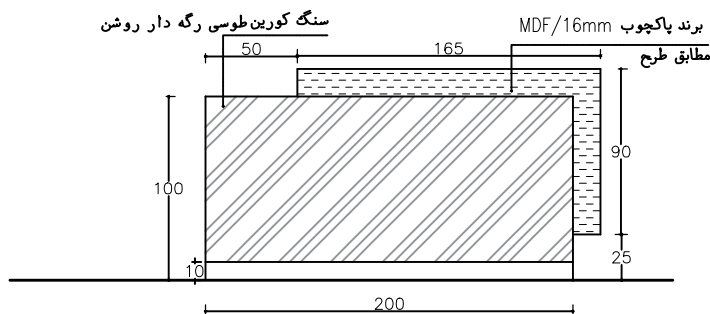

کانتر پذیرایی

VIEW-C
SC 1:10

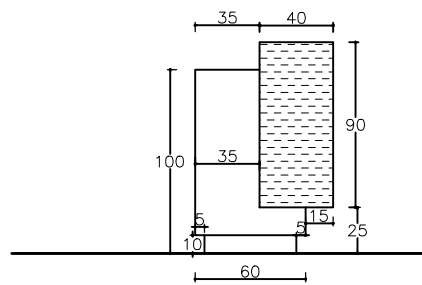


کانتر پذیرایی

VIEW-D
SC 1:10

توجه:

پیمانکار موظف است قبل از اجرا اندازه های وضع موجود را برداشت کرده و با طرح تطبیق دهد.

پیمانکار موظف است قبل از اجرا نمونه تمامی متریال های مصرفی را به تایید طراح و ناظر برساند.

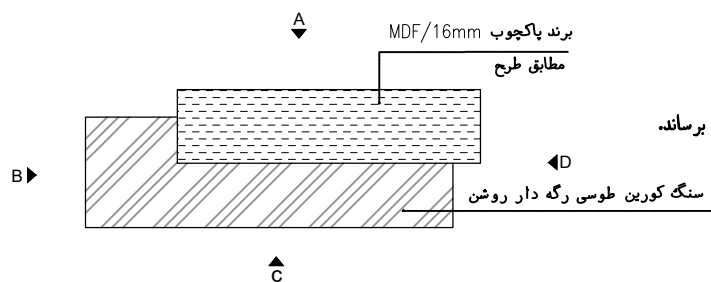


پلان کانتر پذیرایی

SC 1:10


تجهیزات		پانک هلت - اداره کل مهندسی ساختمان (واحد طراحی و نظارت)		
تاریخ	امضاء	تاریخ	امضاء	
شماره کادربرداری:		عنوان پروژه: طبقه منفی یک ساختمان مرکزی فرصت		طوبس: طبق نقشه
معماری		عنوان نقشه: طراحی لابی طبقه منفی یک فرصت		شماره نقشه: A-10
تاریخ	امضاء	تاریخ	امضاء	
۱۳۹۶/۴/۹	امیری زاده	طراح	امیری زاده	
۱۳۹۶/۴/۹	امیری زاده	ترسیم	امیری زاده	
		کنترل		
		تصویب		

سرامیک برند PMA مطابق طرح با تایید طرح و ناظر

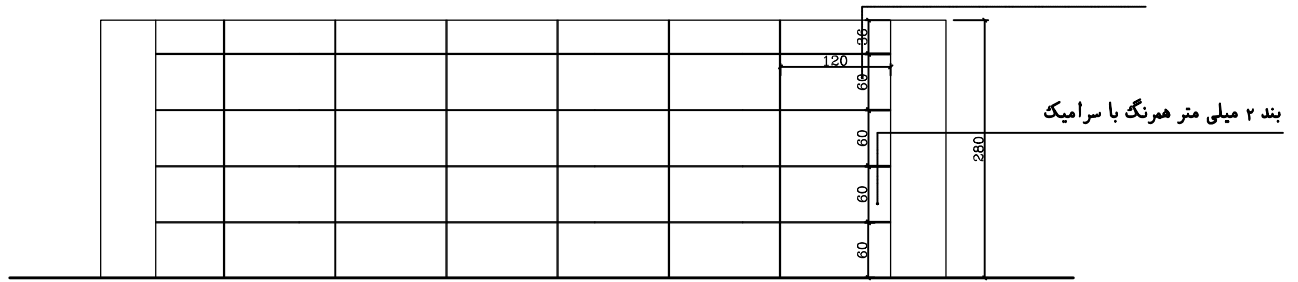


زیر سازی دیوار آبنما

SCALE 1:20

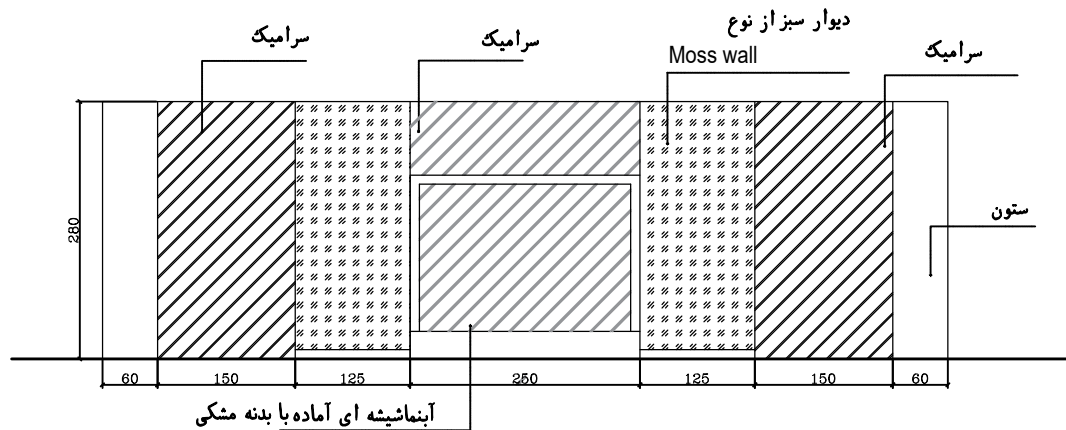

نما دیوار آبنما

SCALE 1:20

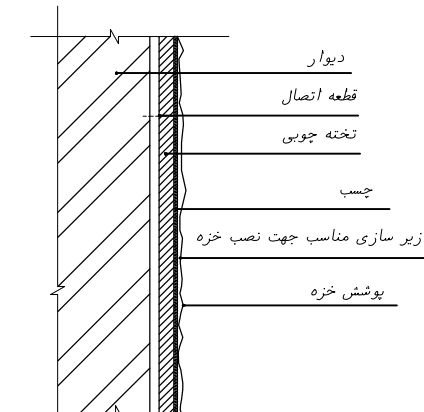


جزئیات اجرایی Moss wall

SCALE 1:10

توجه:

پیمانکار موظف است قبل از اجرا اندازه های وضع موجود را برداشت کرده و با طرح تطبیق دهد.
خرید و نصب آبنما مدل شیشه ای به ابعاد ۲×۲٫۵ متر به عهده پیمانکار میباشد.
خرید و نصب ماس وال به عهده پیمانکار میباشد.
پیمانکار موظف است قبل از اجرا نمونه تمامی متريال های مصرفی را به تایید طراح و ناظر پروژه برساند.

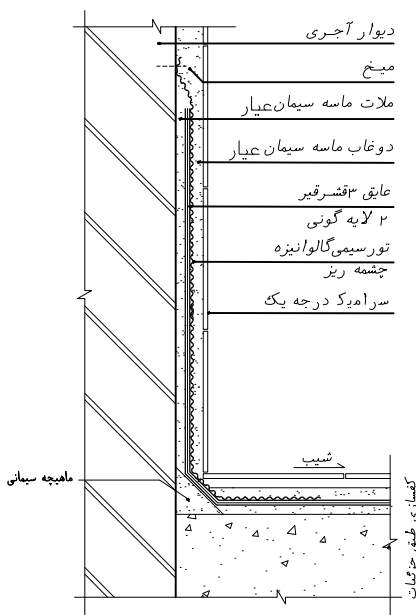

جزئیات اجرایی دیوار در مجاورت سطوح مرطوب

SCALE 1:10

تأیید		تاریخ		امضاء		تاریخ		امضاء	
پاکت هلت - اداره کل مهندسی ساختمان (واحد طراحی و نظارت)		شماره کارپروژه:		رقشه:		معماری		تاریخ	
عنوان پروژه: طبقه منفی یک ساختمان مرکزی فرصت		طراح: امیری زاده		ترسیم: امیری زاده		کنترل: امیری زاده		تصویر: امیری زاده	
عنوان نقشه: طراحی لابی طبقه منفی یک فرصت		طراح: امیری زاده		ترسیم: امیری زاده		کنترل: امیری زاده		تصویر: امیری زاده	
شماره نقشه: A-11		طراح: امیری زاده		ترسیم: امیری زاده		کنترل: امیری زاده		تصویر: امیری زاده	

جدول نازک‌کاری

ردیف	شرح فضا	پوشش نهائی گسارزی	پوشش نهائی بالای ازاره دیوار	پوشش نهائی بالای ازاره دیوار	رنگ آمیزی دیوار	سقف اصلی	سقف گالوپ	رنگ آمیزی سقف	یاد آوری
①	ورودی	حفظ وضع موجود سرامیک و تمویض موکت موجود با موکت درجه یک برند ترک	قرنیز پی وی سی به رنگ ذغالی به ارتفاع ۱۰ سانتی متر	مطابق جزئیات دیوار ها	_____	_____	حفظ وضع موجود + ترمیم و رنگ آمیزی	رنگ پلاستیک پارس بهار کدرنگ ۴۱۰	_____
②	پذیرش	حفظ وضع موجود سرامیک و تمویض موکت موجود با موکت درجه یک برند ترک	قرنیز پی وی سی به رنگ ذغالی به ارتفاع ۱۰ سانتی متر	مطابق جزئیات دیوار ها	_____	_____	حفظ وضع موجود + ترمیم و رنگ آمیزی	رنگ پلاستیک پارس بهار کدرنگ ۴۱۰	_____
③	فضای انتظار	حفظ وضع موجود سرامیک و تمویض موکت موجود با موکت درجه یک برند ترک	قرنیز پی وی سی به رنگ ذغالی به ارتفاع ۱۰ سانتی متر	مطابق جزئیات دیوار ها	_____	_____	حفظ وضع موجود + ترمیم و رنگ آمیزی	رنگ پلاستیک پارس بهار کدرنگ ۴۱۰	_____
④	دیوار E, F	_____	قرنیز پی وی سی به رنگ ذغالی به ارتفاع ۱۰ سانتی متر	کاغذ دیواری درجه یک به رنگ طوسی روشن	_____	_____	_____	_____	_____
⑤	دیوار A, B	_____	قرنیز پی وی سی به رنگ ذغالی به ارتفاع ۱۰ سانتی متر	لمسه کوبی پارچه مخمل و استیل مطابق جزئیات دیوار ها	_____	_____	_____	_____	_____
⑥	دیوار D, C	_____	قرنیز پی وی سی به رنگ ذغالی به ارتفاع ۱۰ سانتی متر	مطابق جزئیات دیوار ها	_____	_____	_____	_____	_____
⑦	فضای آسانسور	_____	قرنیز پی وی سی به رنگ ذغالی به ارتفاع ۱۰ سانتی متر	مطابق جزئیات دیوار ها	_____	_____	_____	_____	_____

توجه:

ساخت باغچه ترئینی با U چوبی MDF پاکچوب به رنگ مشکی مات (به ضلع ۱۰ سانتی متر)
کف باغچه چمن مصنوعی اجرا گردد و با سنگ رودخانه ای سفید پر گردد.

توجه:

جهت تلویزیون و یخچال و دستگاه قهوه ساز و آبما پرز برق با سرخط مجزا از تابلوی برق در نظر گرفته شود.

پیمانکار موظف است قبل از اجرا اندازه های وضع موجود را

برداشت کرده و با طرح تطبیق دهد.

چراغ خطی با عرض ۶ سانتی متر در محل های مشخص شده اجرا گردد.


یاد آوری:

-کلیه مصالح مصرفی از نوع مرغوب می باشد.

کلیه ابعاد قبل از ساخت با وضع موجود چک شود.

کلیه MDF مصرفی از برند پاکچوب باشد و قبل از اجرا به تایید طراح و ناظر پروژه برسد

در صورت عدم موجودی مصالح موجود در جدول نازککاری پیمانکار موظف است نسبت به تهیه و اجرای مصالح مشابه با هماهنگی و تایید ناظر پروژه اقدام نماید.

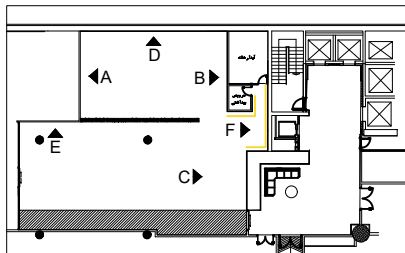

پلان راهنما

آبعاد فضا: 42.00x29.70cm رنگ: مصماری		آبعاد فضا: 42.00x29.70cm رنگ: مصماری		آبعاد فضا: 42.00x29.70cm رنگ: مصماری	
آبعاد فضا: 42.00x29.70cm رنگ: مصماری		آبعاد فضا: 42.00x29.70cm رنگ: مصماری		آبعاد فضا: 42.00x29.70cm رنگ: مصماری	
آبعاد فضا: 42.00x29.70cm رنگ: مصماری		آبعاد فضا: 42.00x29.70cm رنگ: مصماری		آبعاد فضا: 42.00x29.70cm رنگ: مصماری	
آبعاد فضا: 42.00x29.70cm رنگ: مصماری		آبعاد فضا: 42.00x29.70cm رنگ: مصماری		آبعاد فضا: 42.00x29.70cm رنگ: مصماری	